
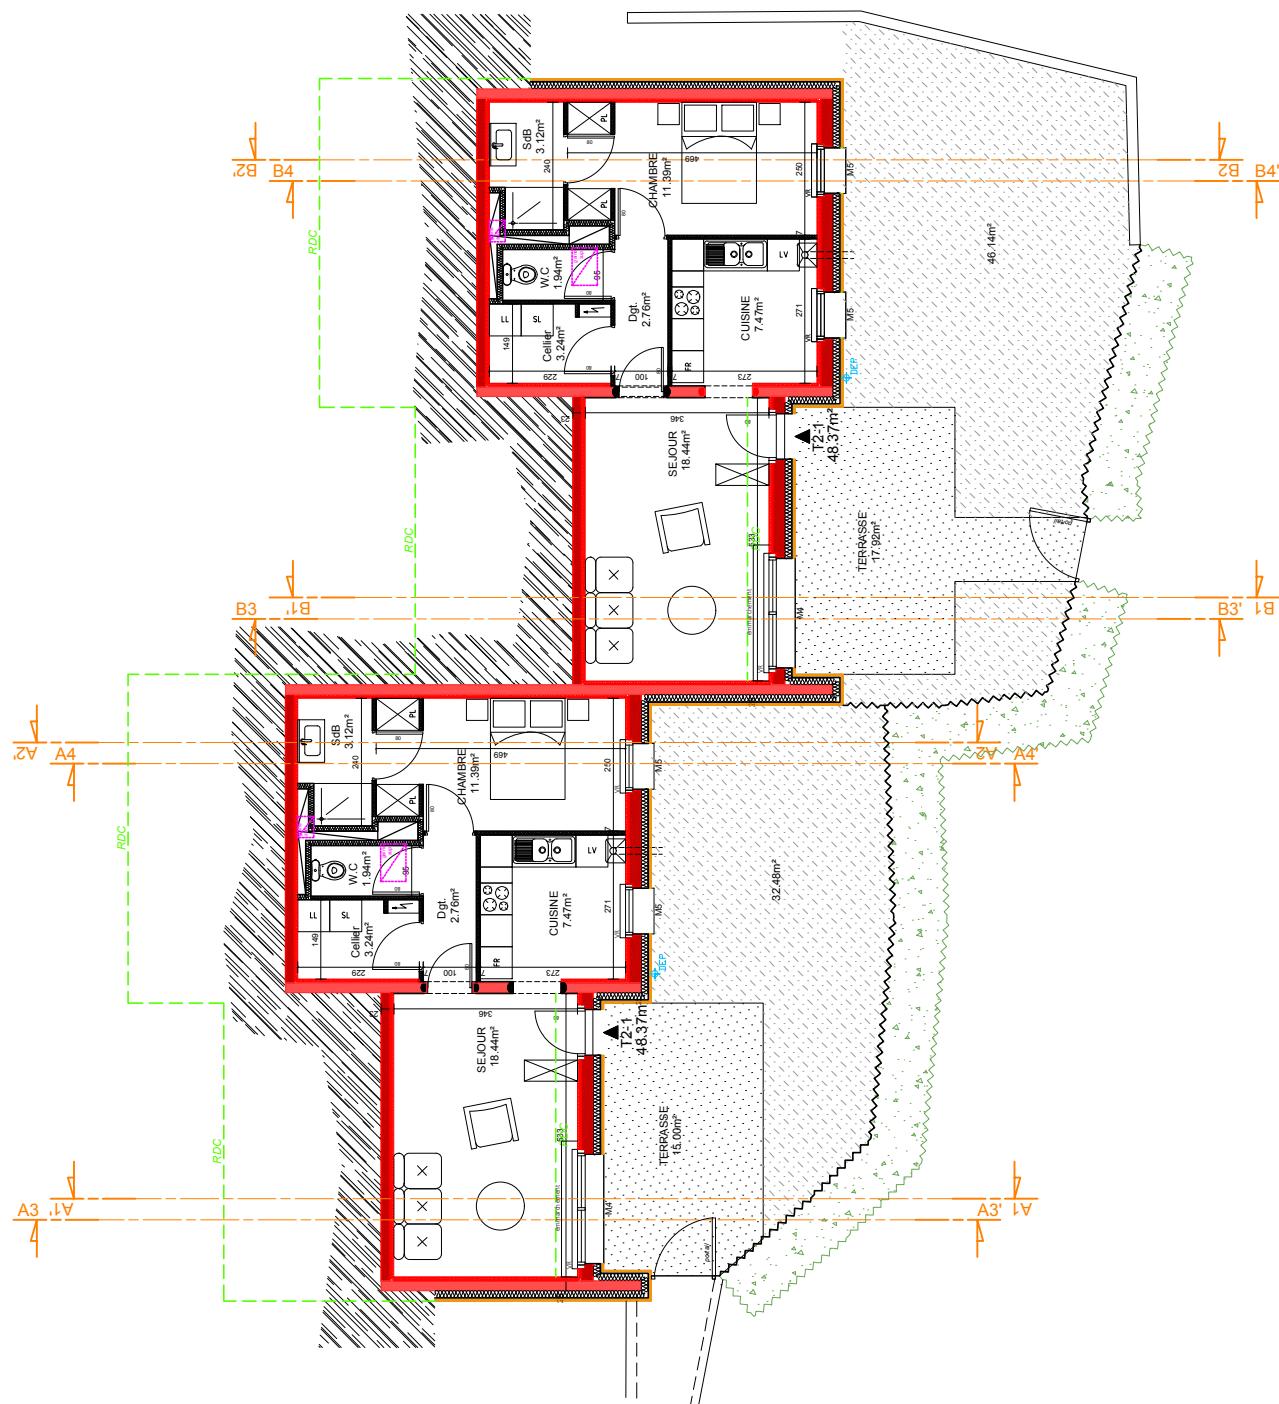


PLAN RDJ - Bâtiment 4 - n°8-10
Ech : 1/100


Ech : 1/100

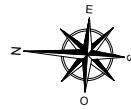

EXISTANT


PLAN RDC - Bâtiment 4 - n°8-10
Ech : 1/100

Ech : 1/100

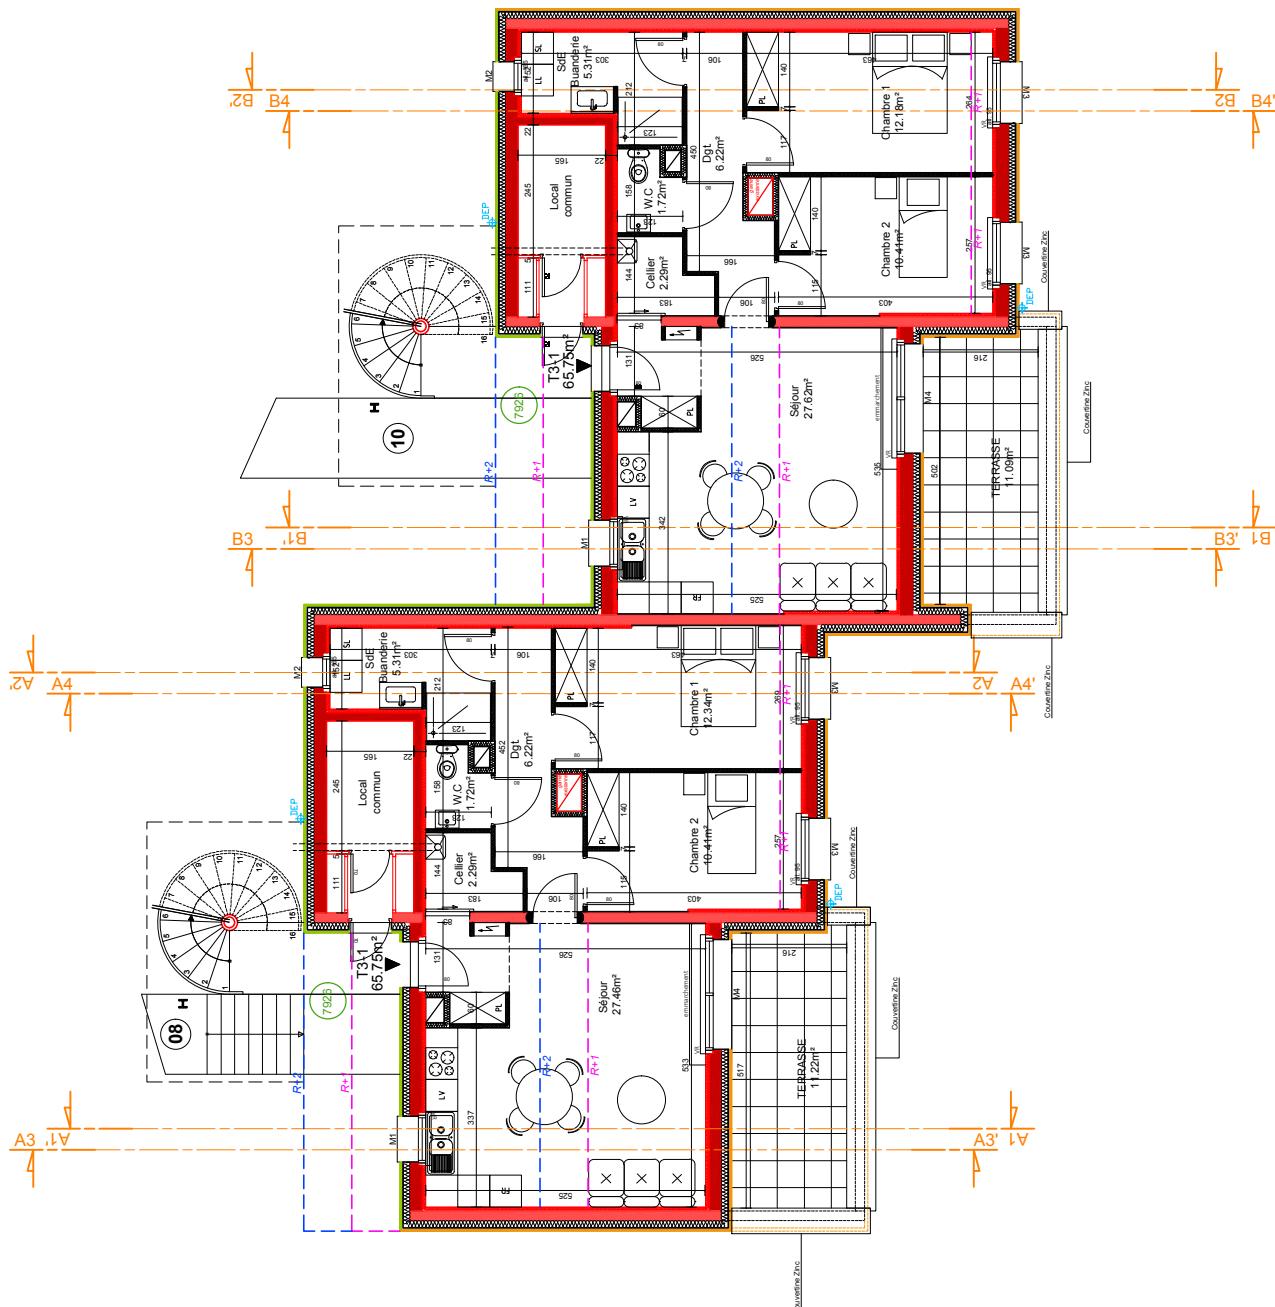


EXISTANT

PLAN R+1 - Bâtiment 4 - n°8-10
Ech : 1/100


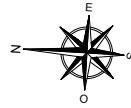


EXISTANT

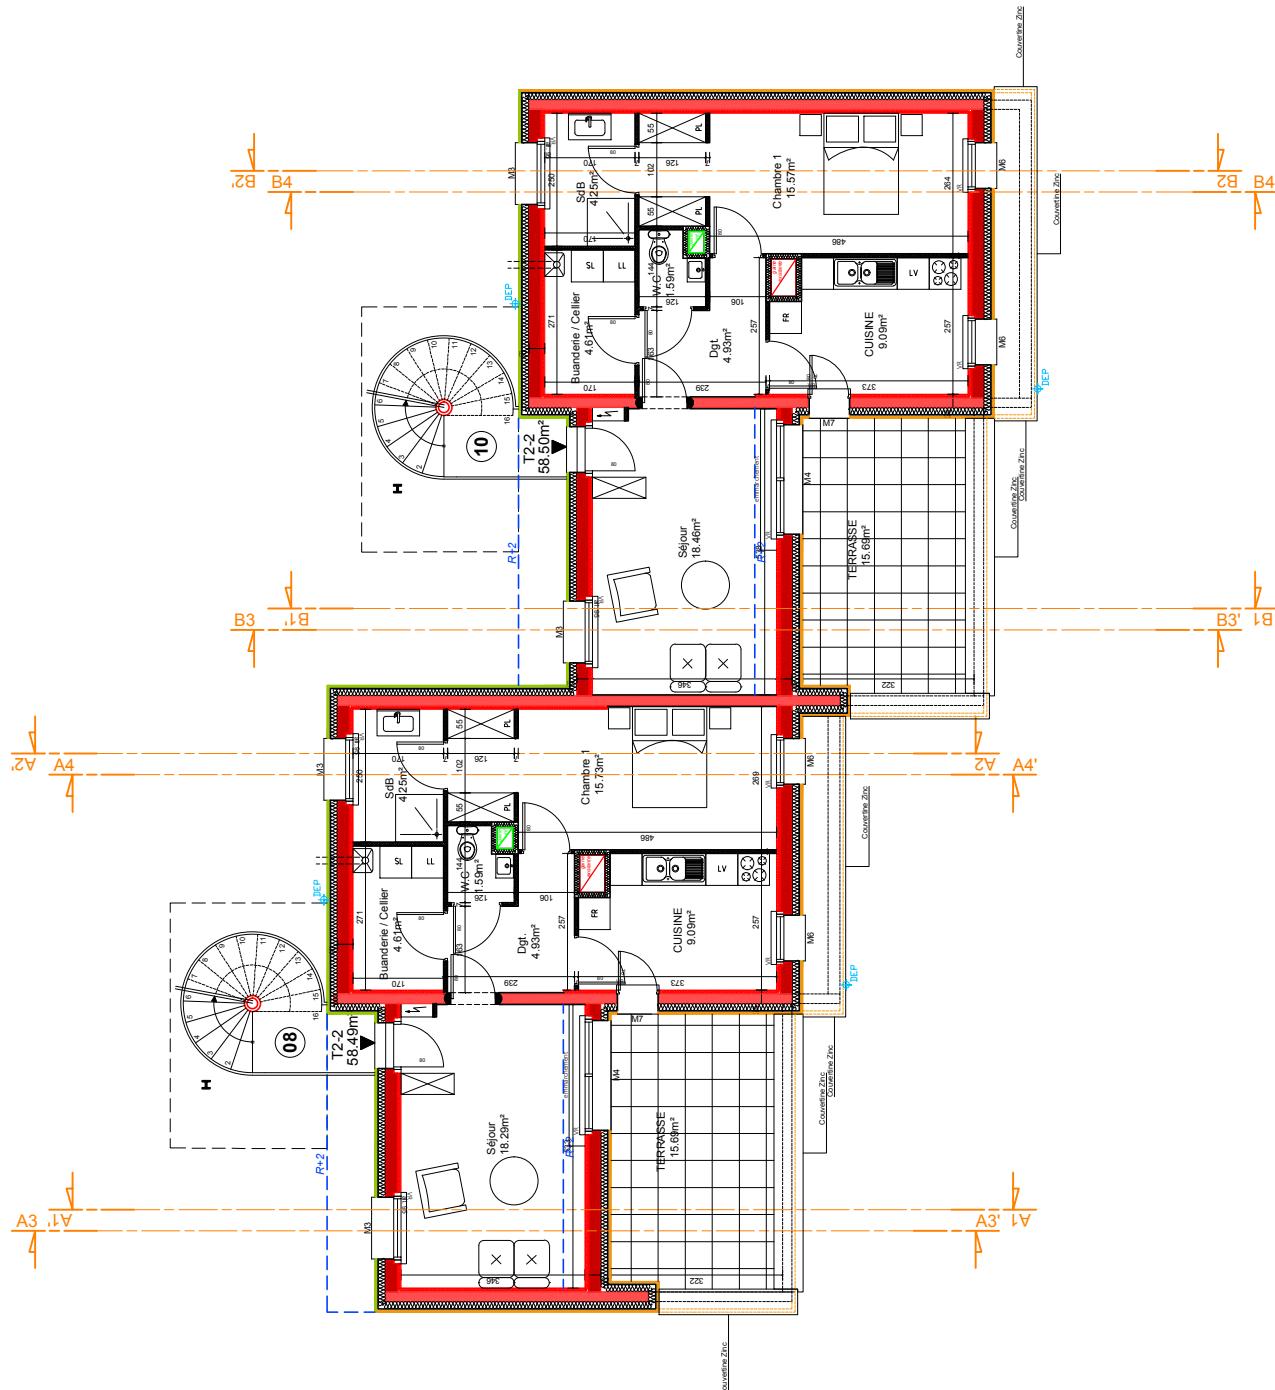


PLAN R+2 - Bâtiment 4 - n°8-10
Ech : 1/100

Ech : 1/100

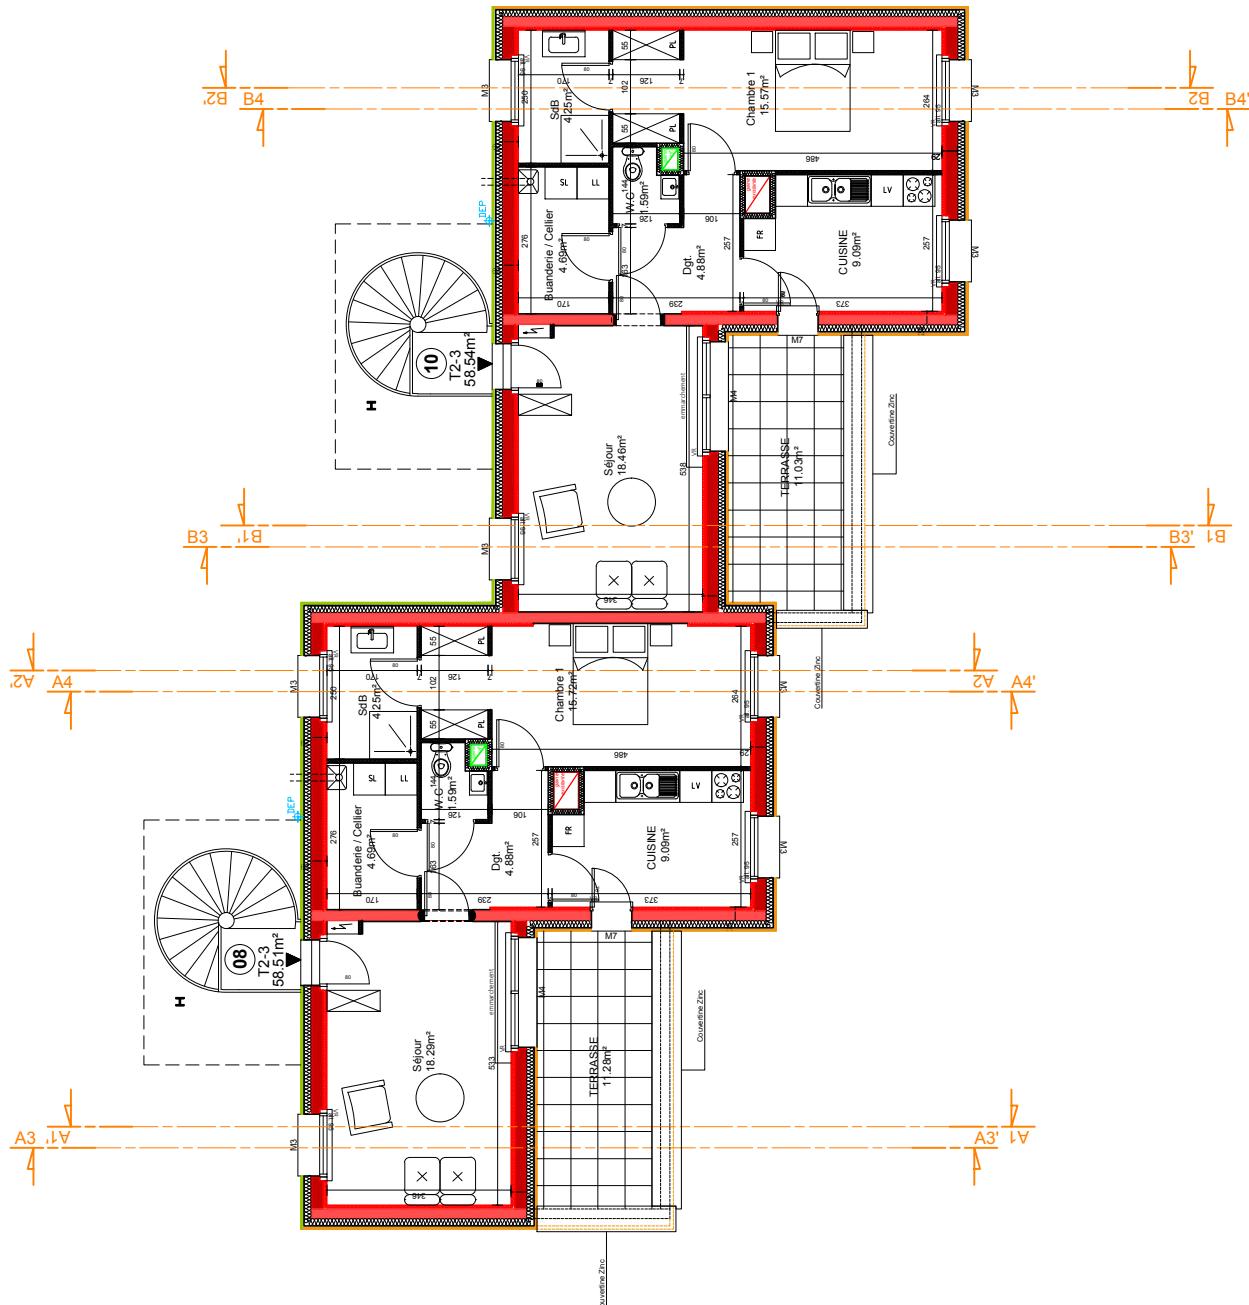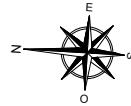

EXISTANT


PLAN DE TOITURE - Bâtiment 4 - n°8-10
Ech : 1/100

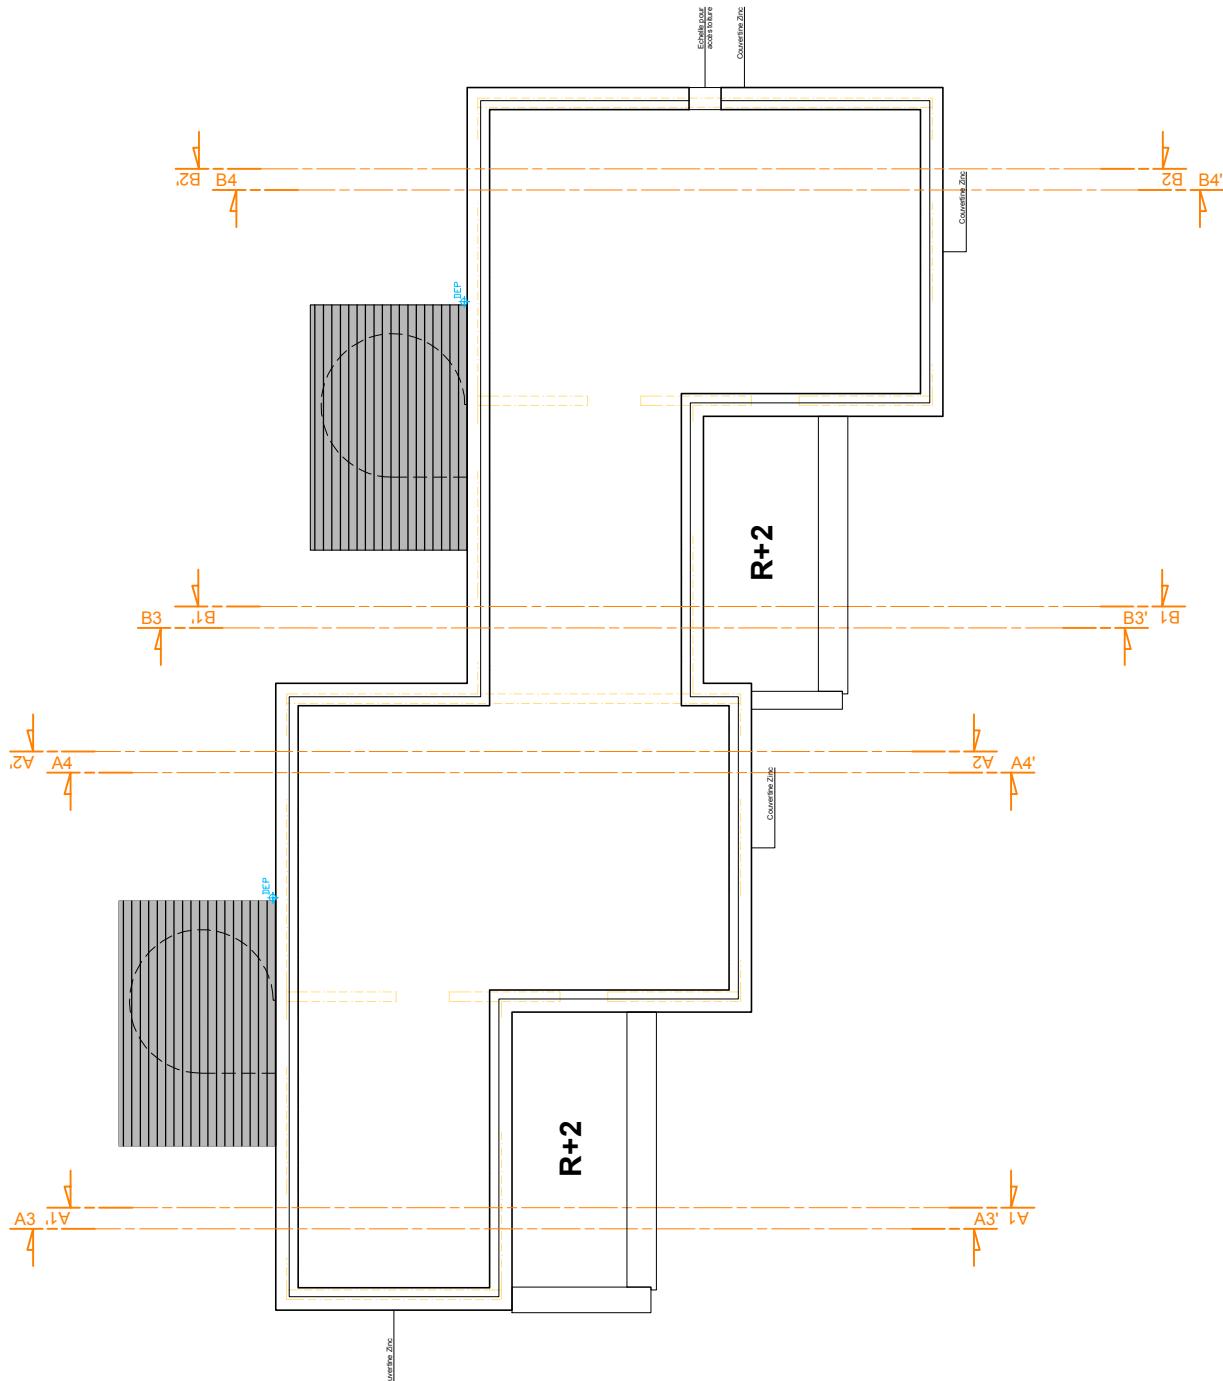

EXISTANT


PLAN RDJ - Bâtiment 4 - n°8

Ech : 1/50

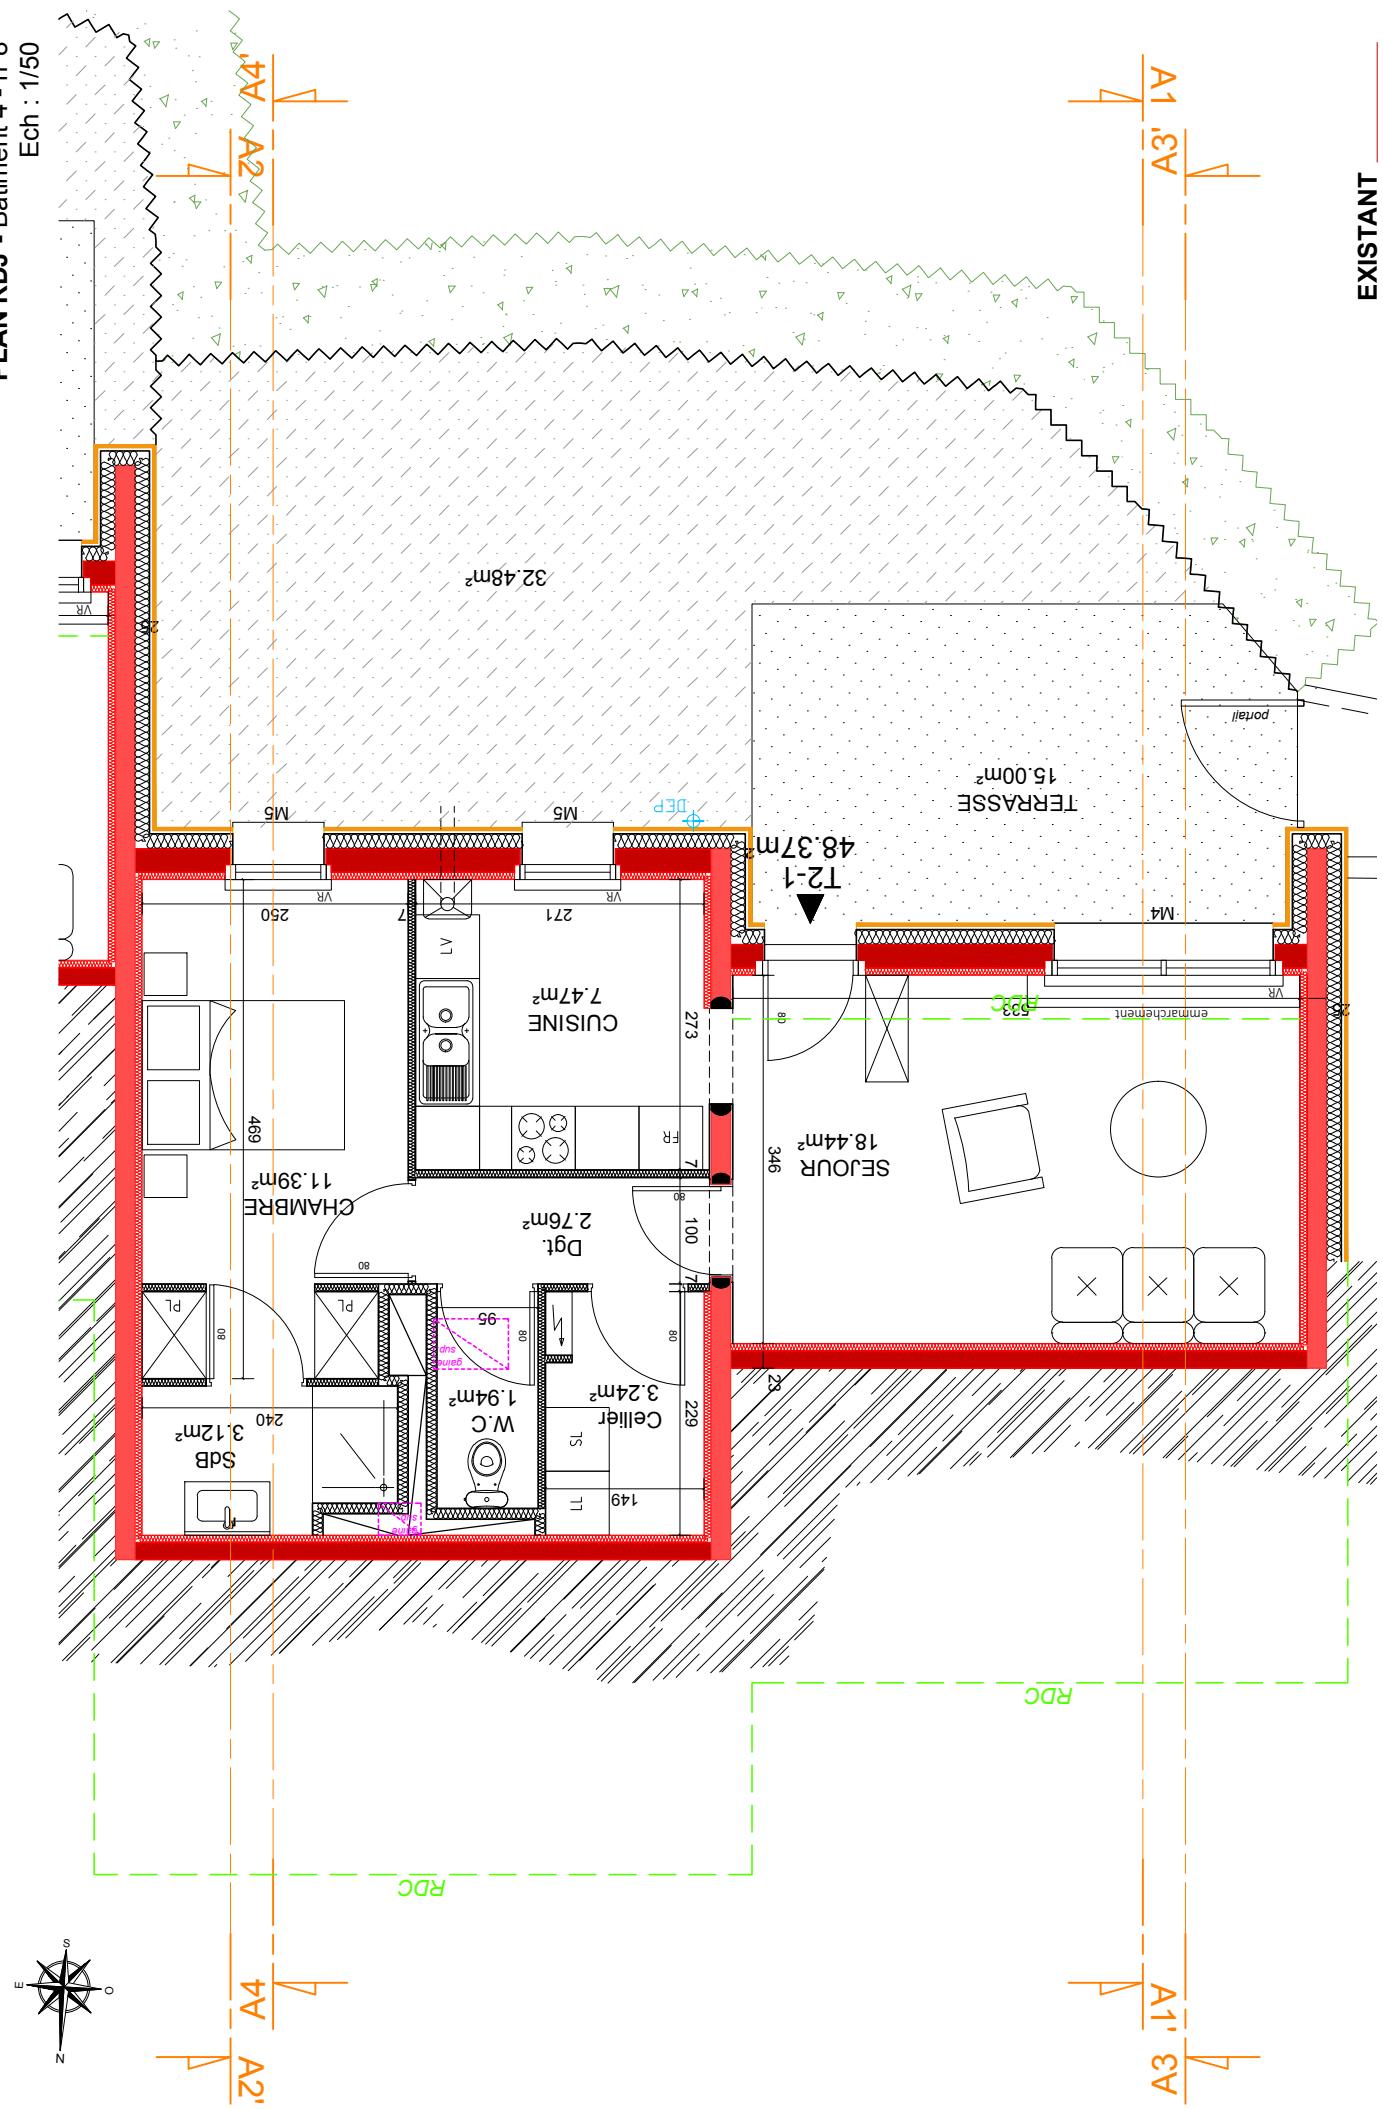


PLAN RDC - Bâtiment 4 - n°8
Ech : 1/50

Ech : 1/50

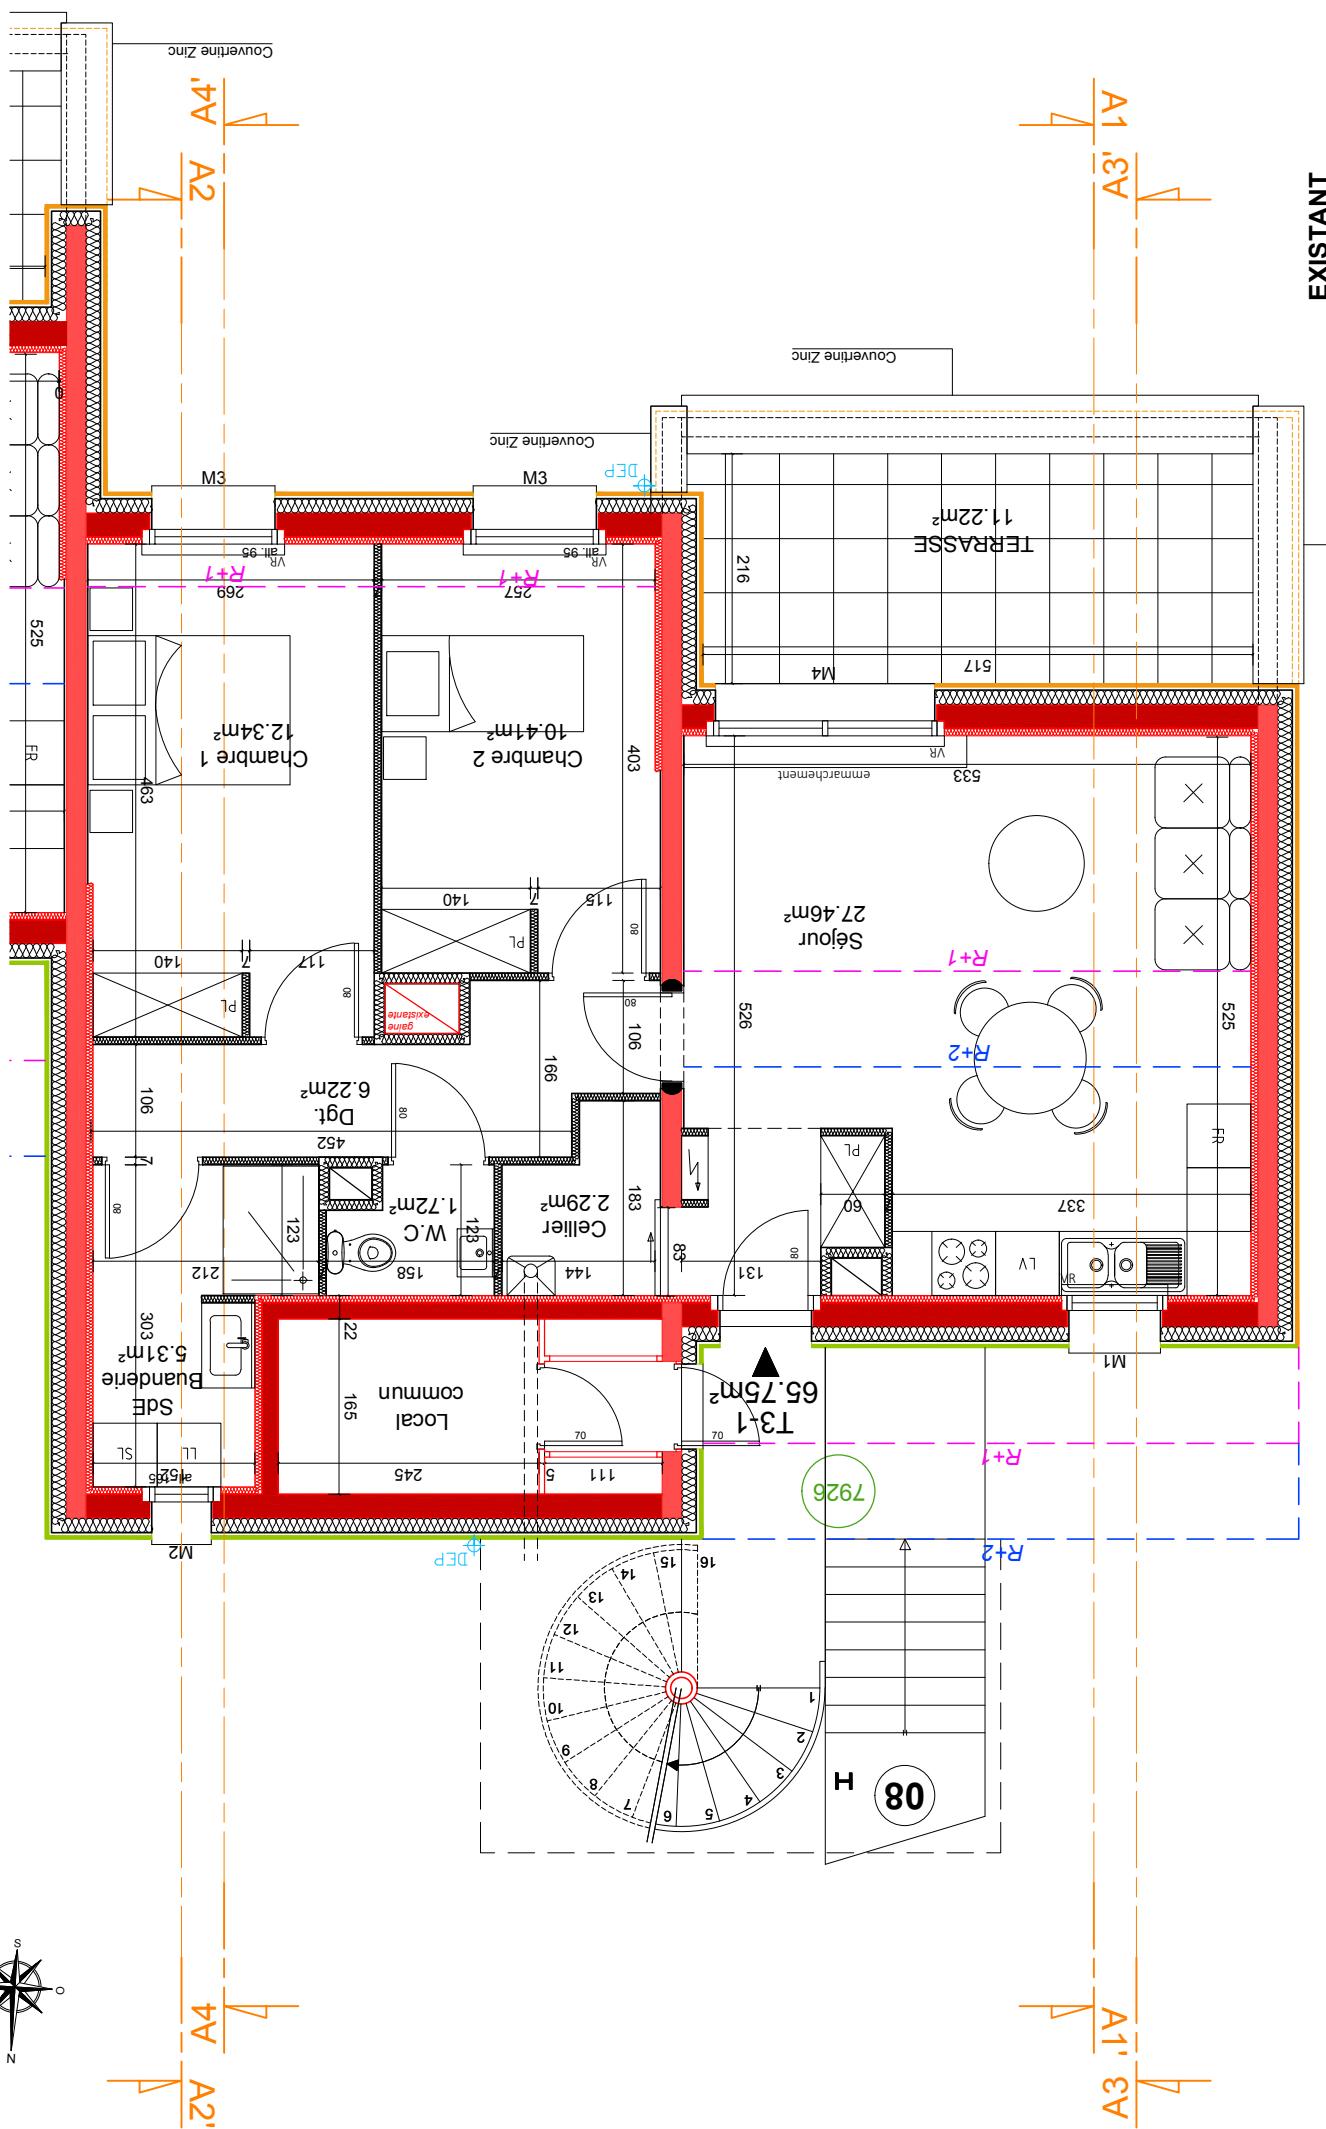


PLAN R+1 - Bâtiment 4 - n°8
Ech : 1/50

Ech : 1/50

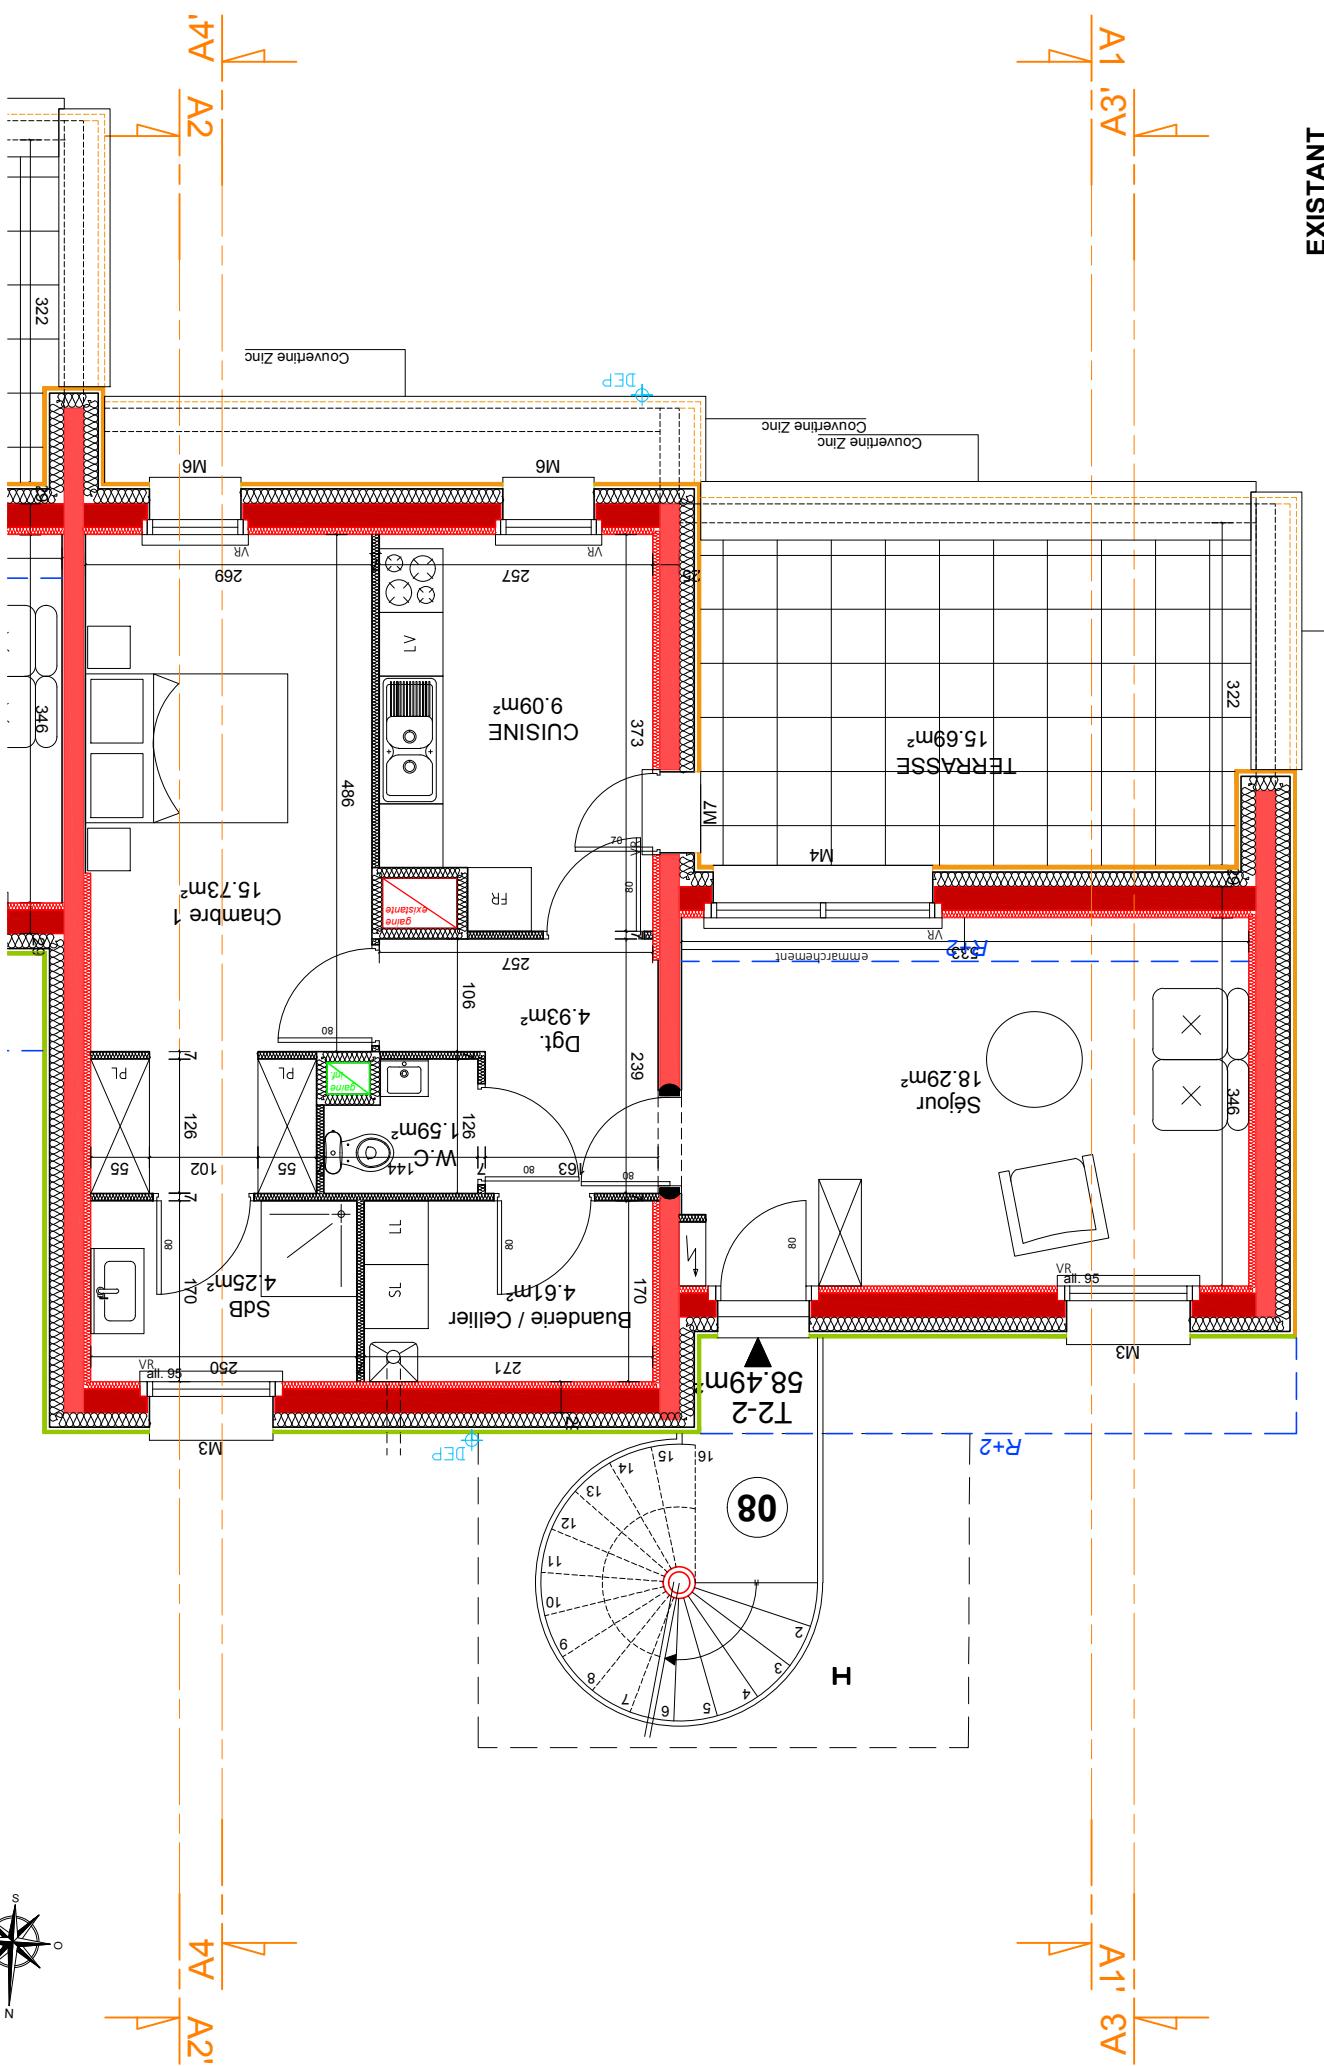


PLAN R+2 - Bâtiment 4 - n°8
Ech : 1/50

Ech : 1/50

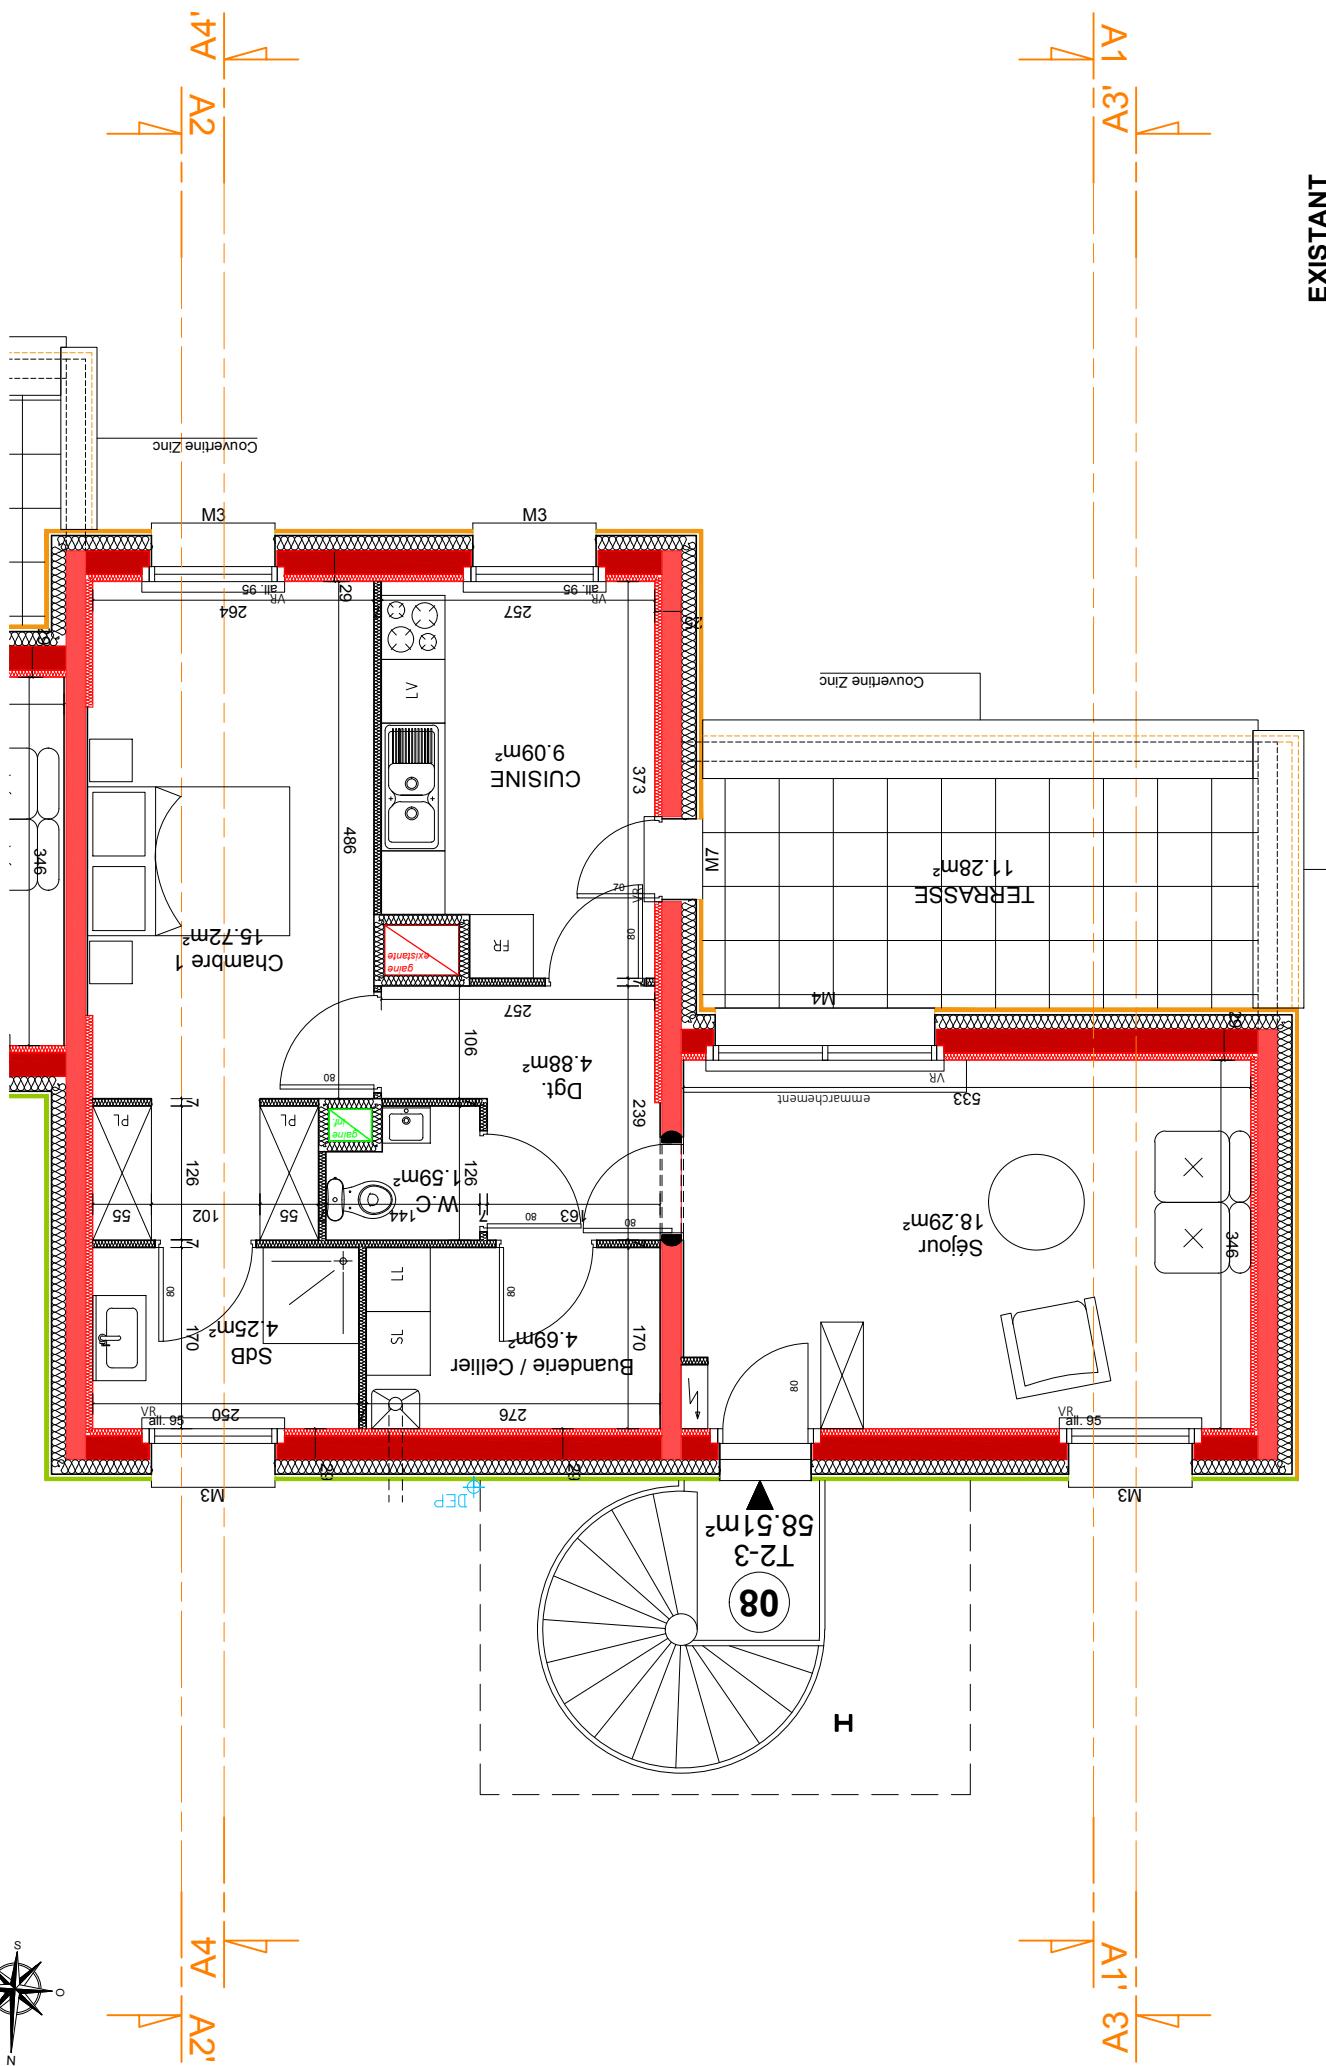


PLAN DE TOITURE - Bâtiment 4 - n°8

Ech : 1/50

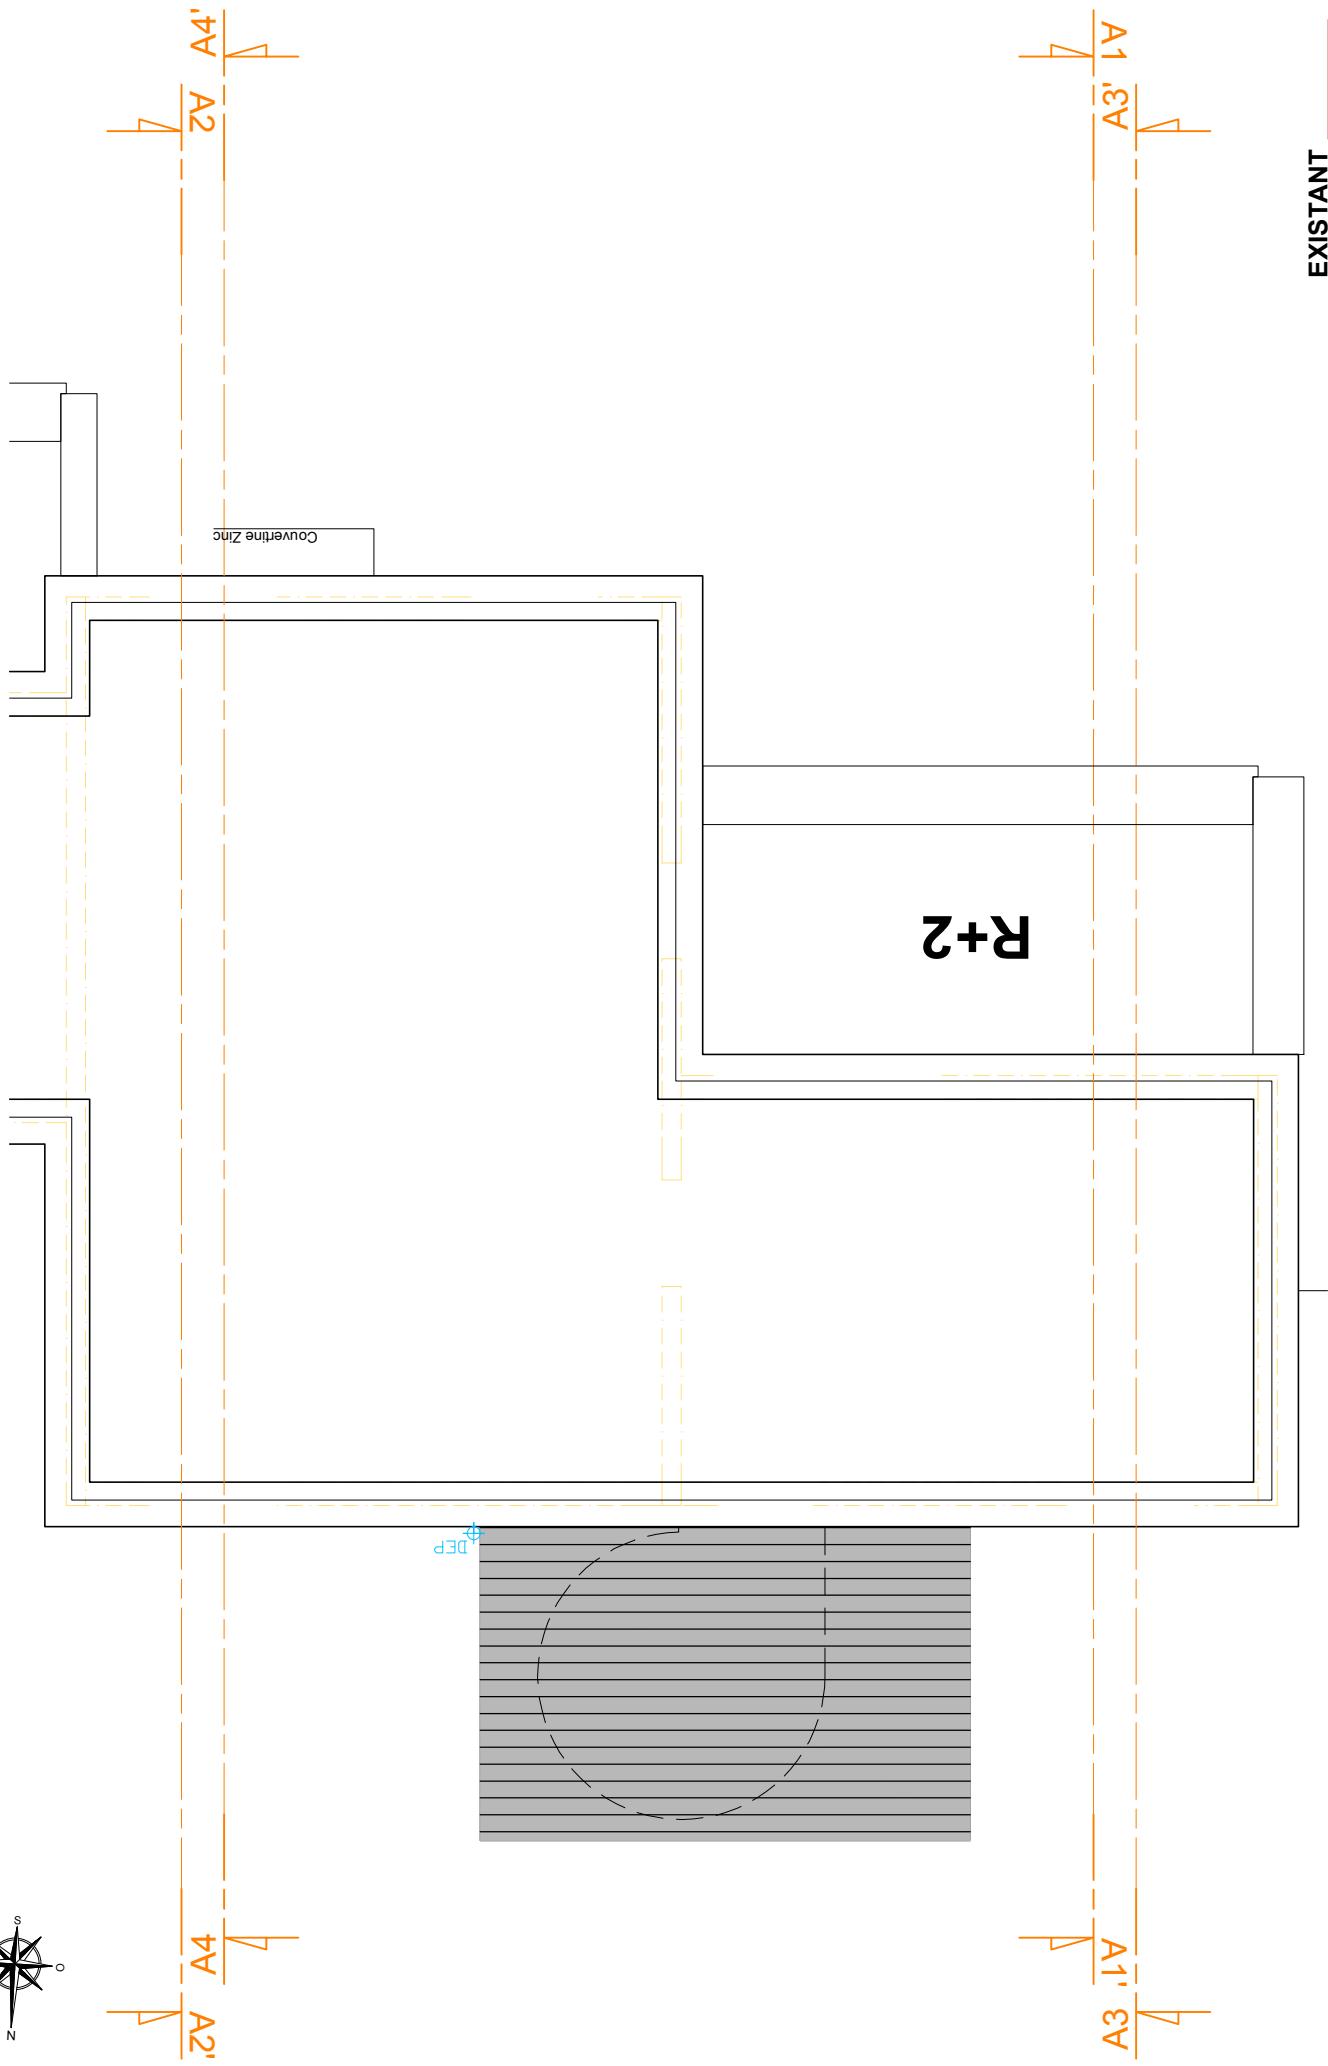


EXISTANT

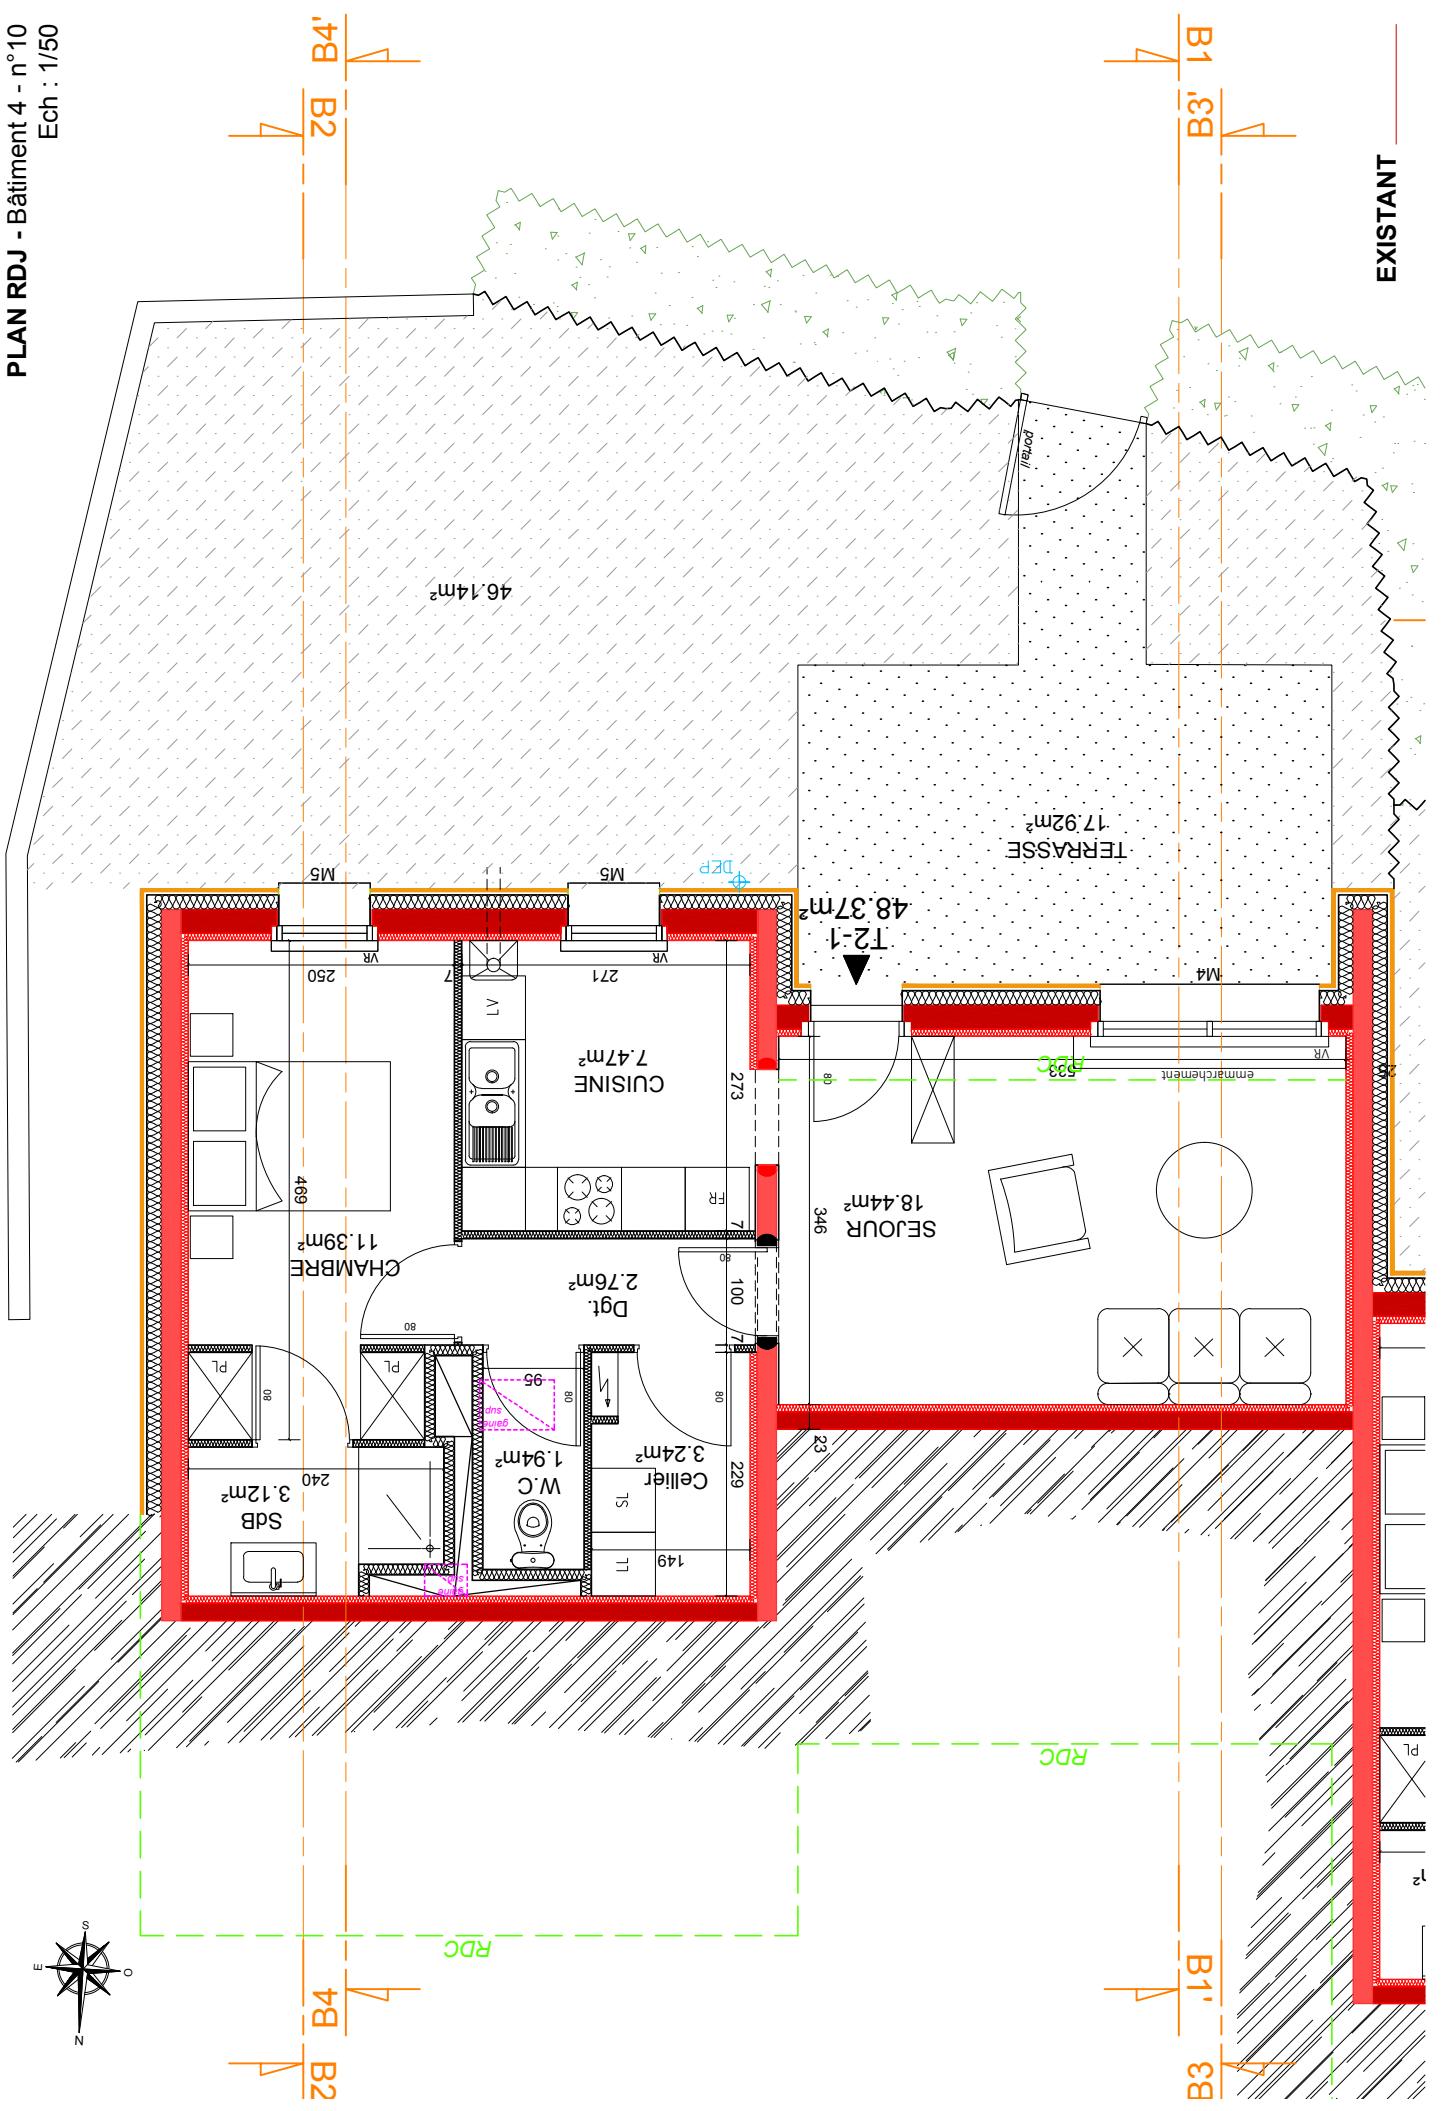


PLAN RDC - Bâtiment 4 - n°10
Ech : 1/50


Ech : 1/50

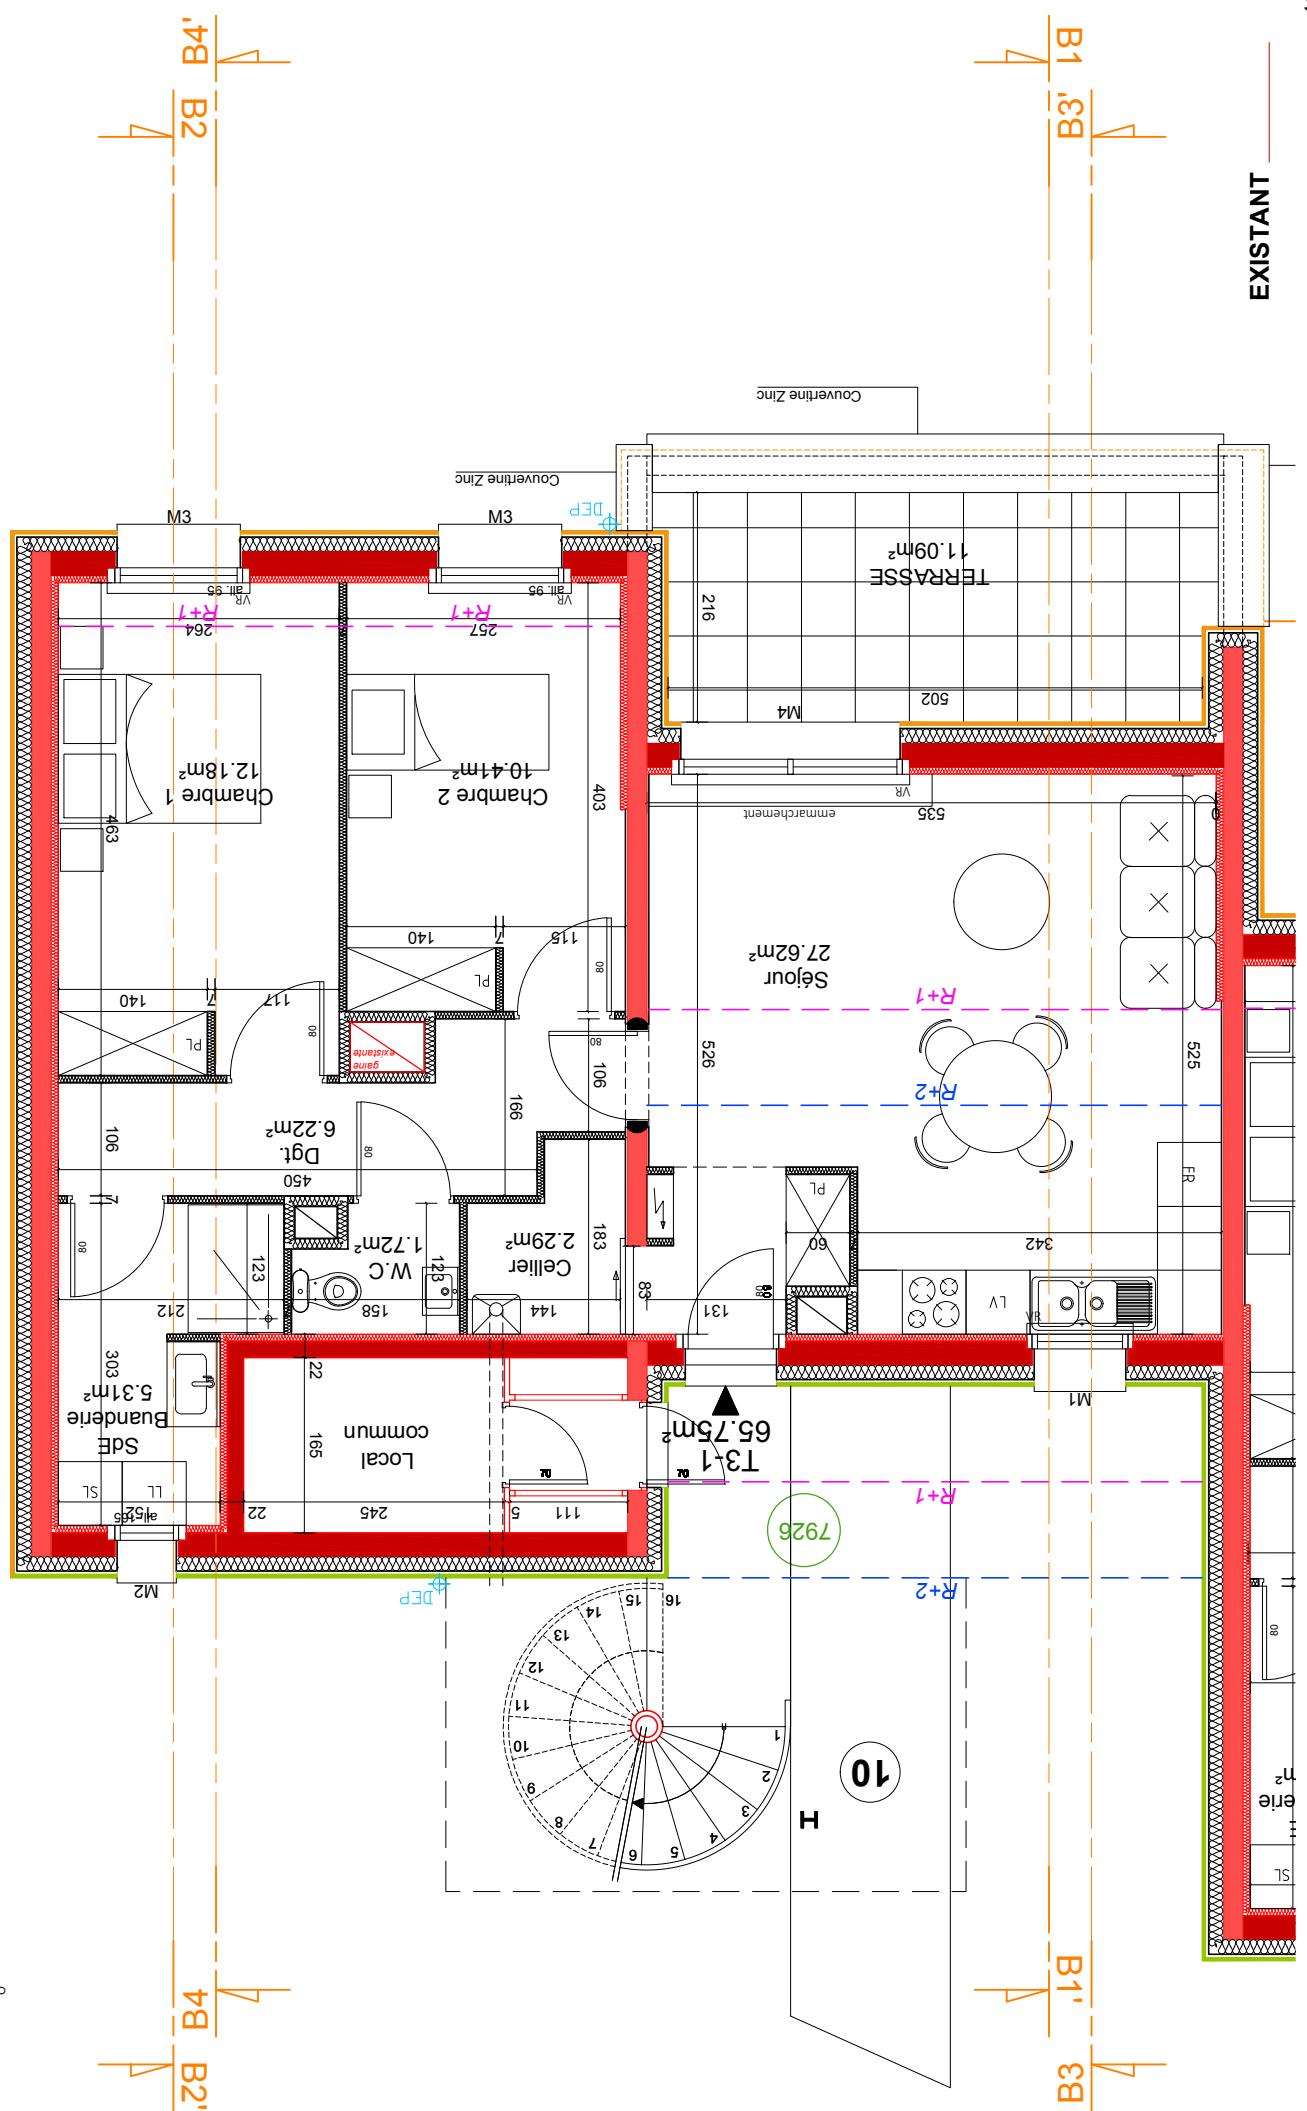

PLAN R+1 - Bâtiment 4 - n°10

Ech : 1/50

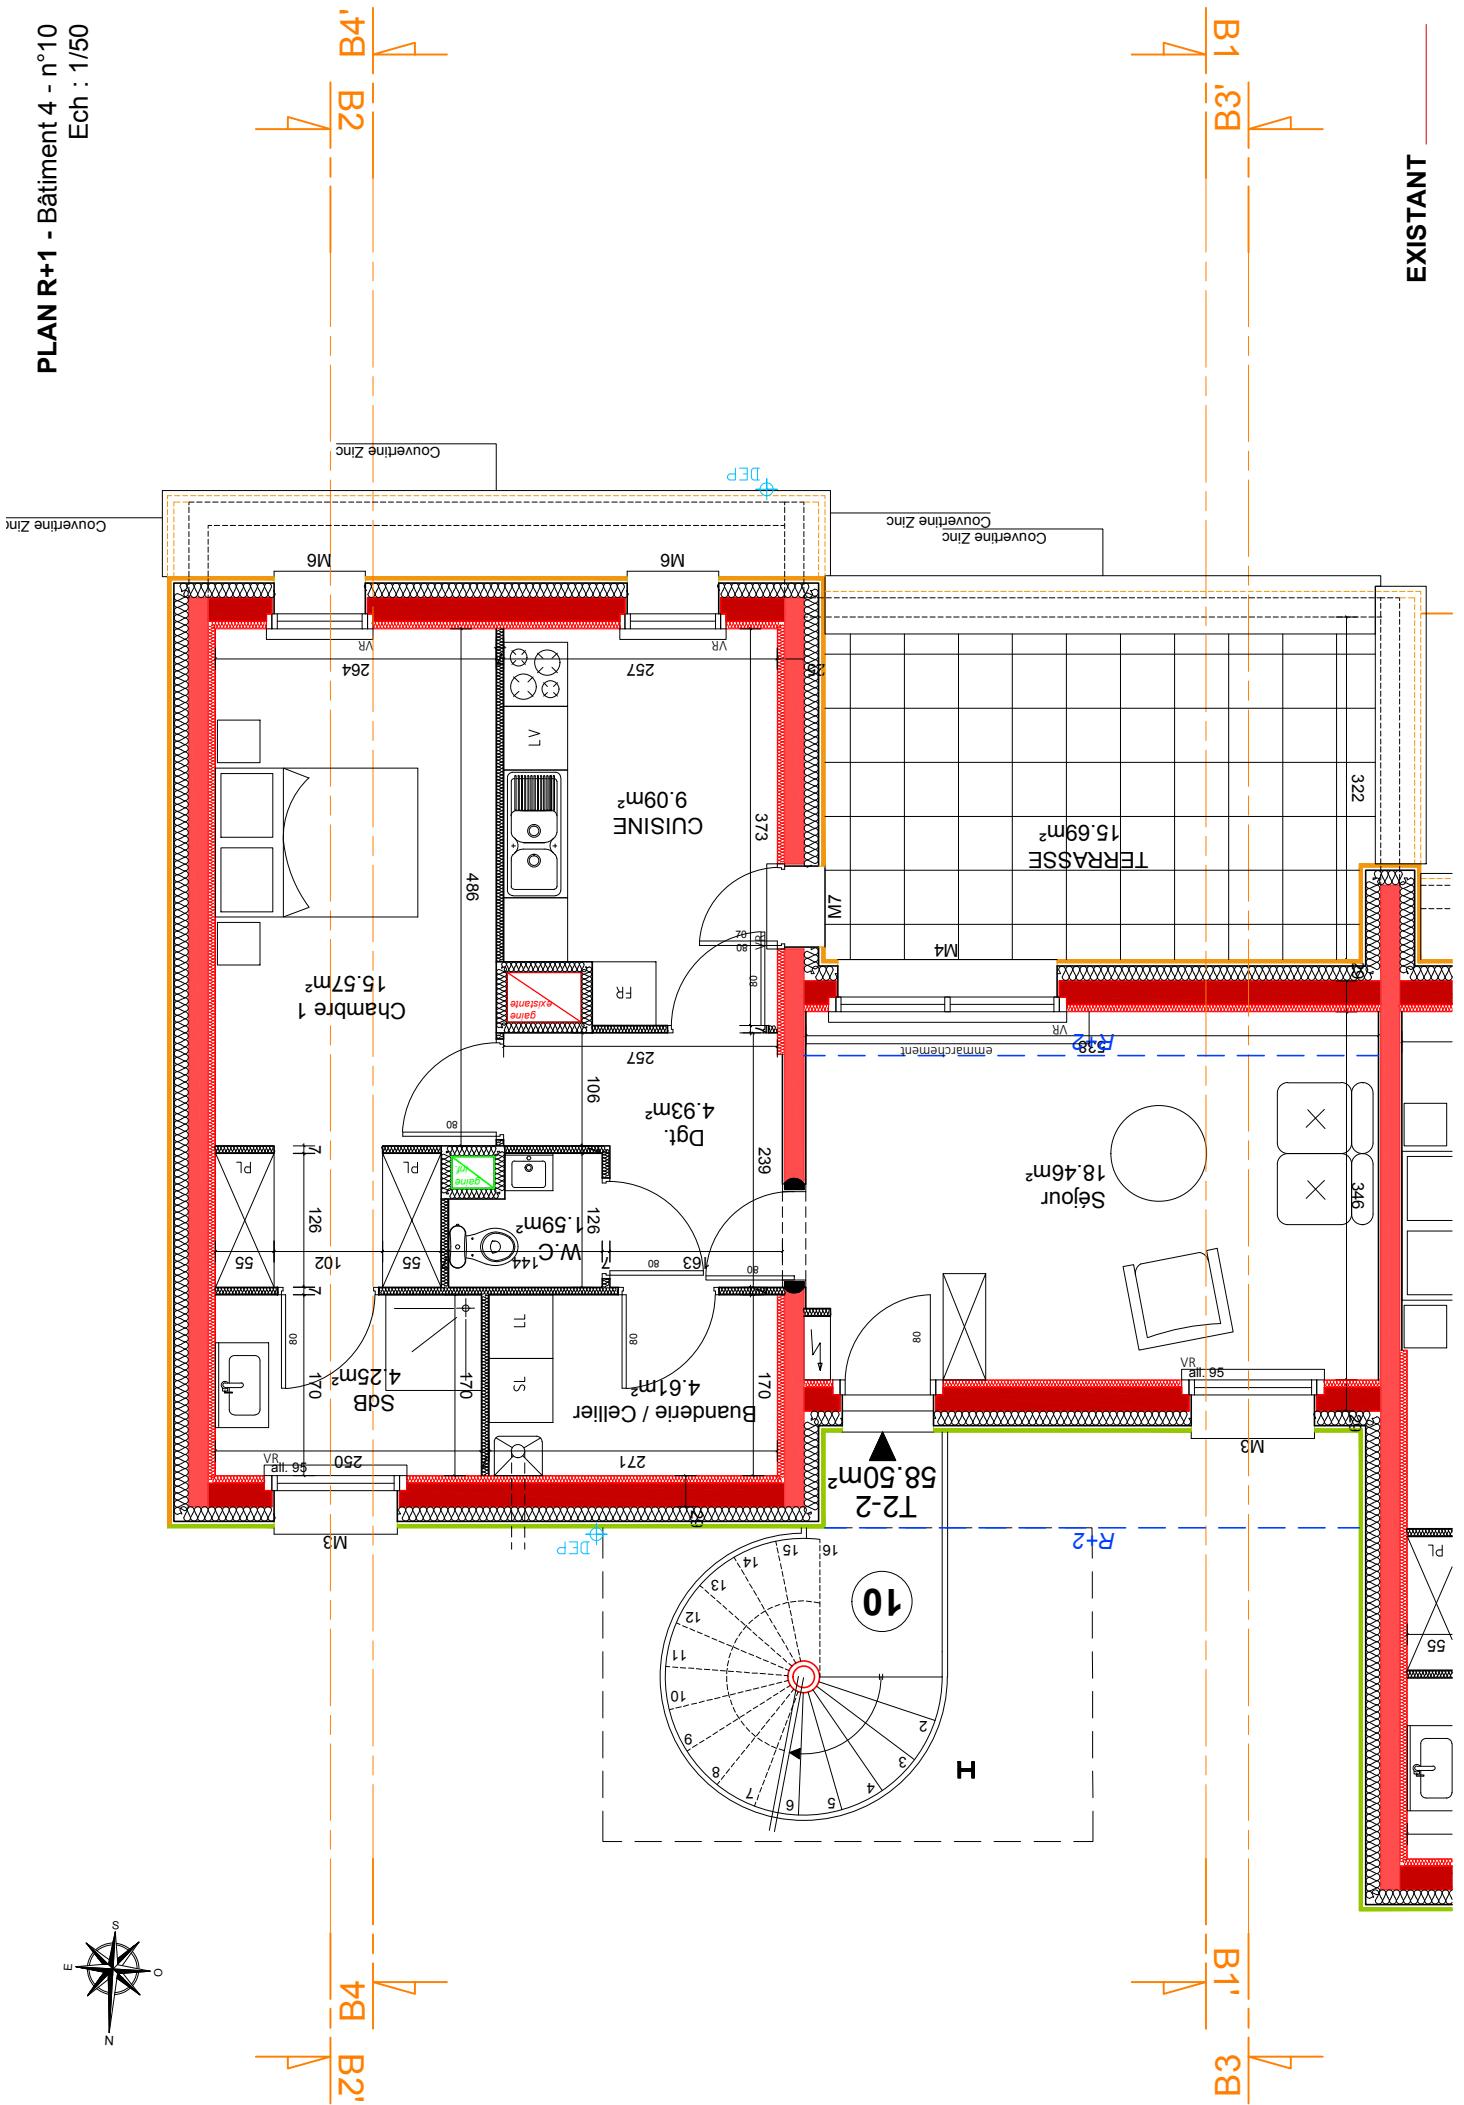


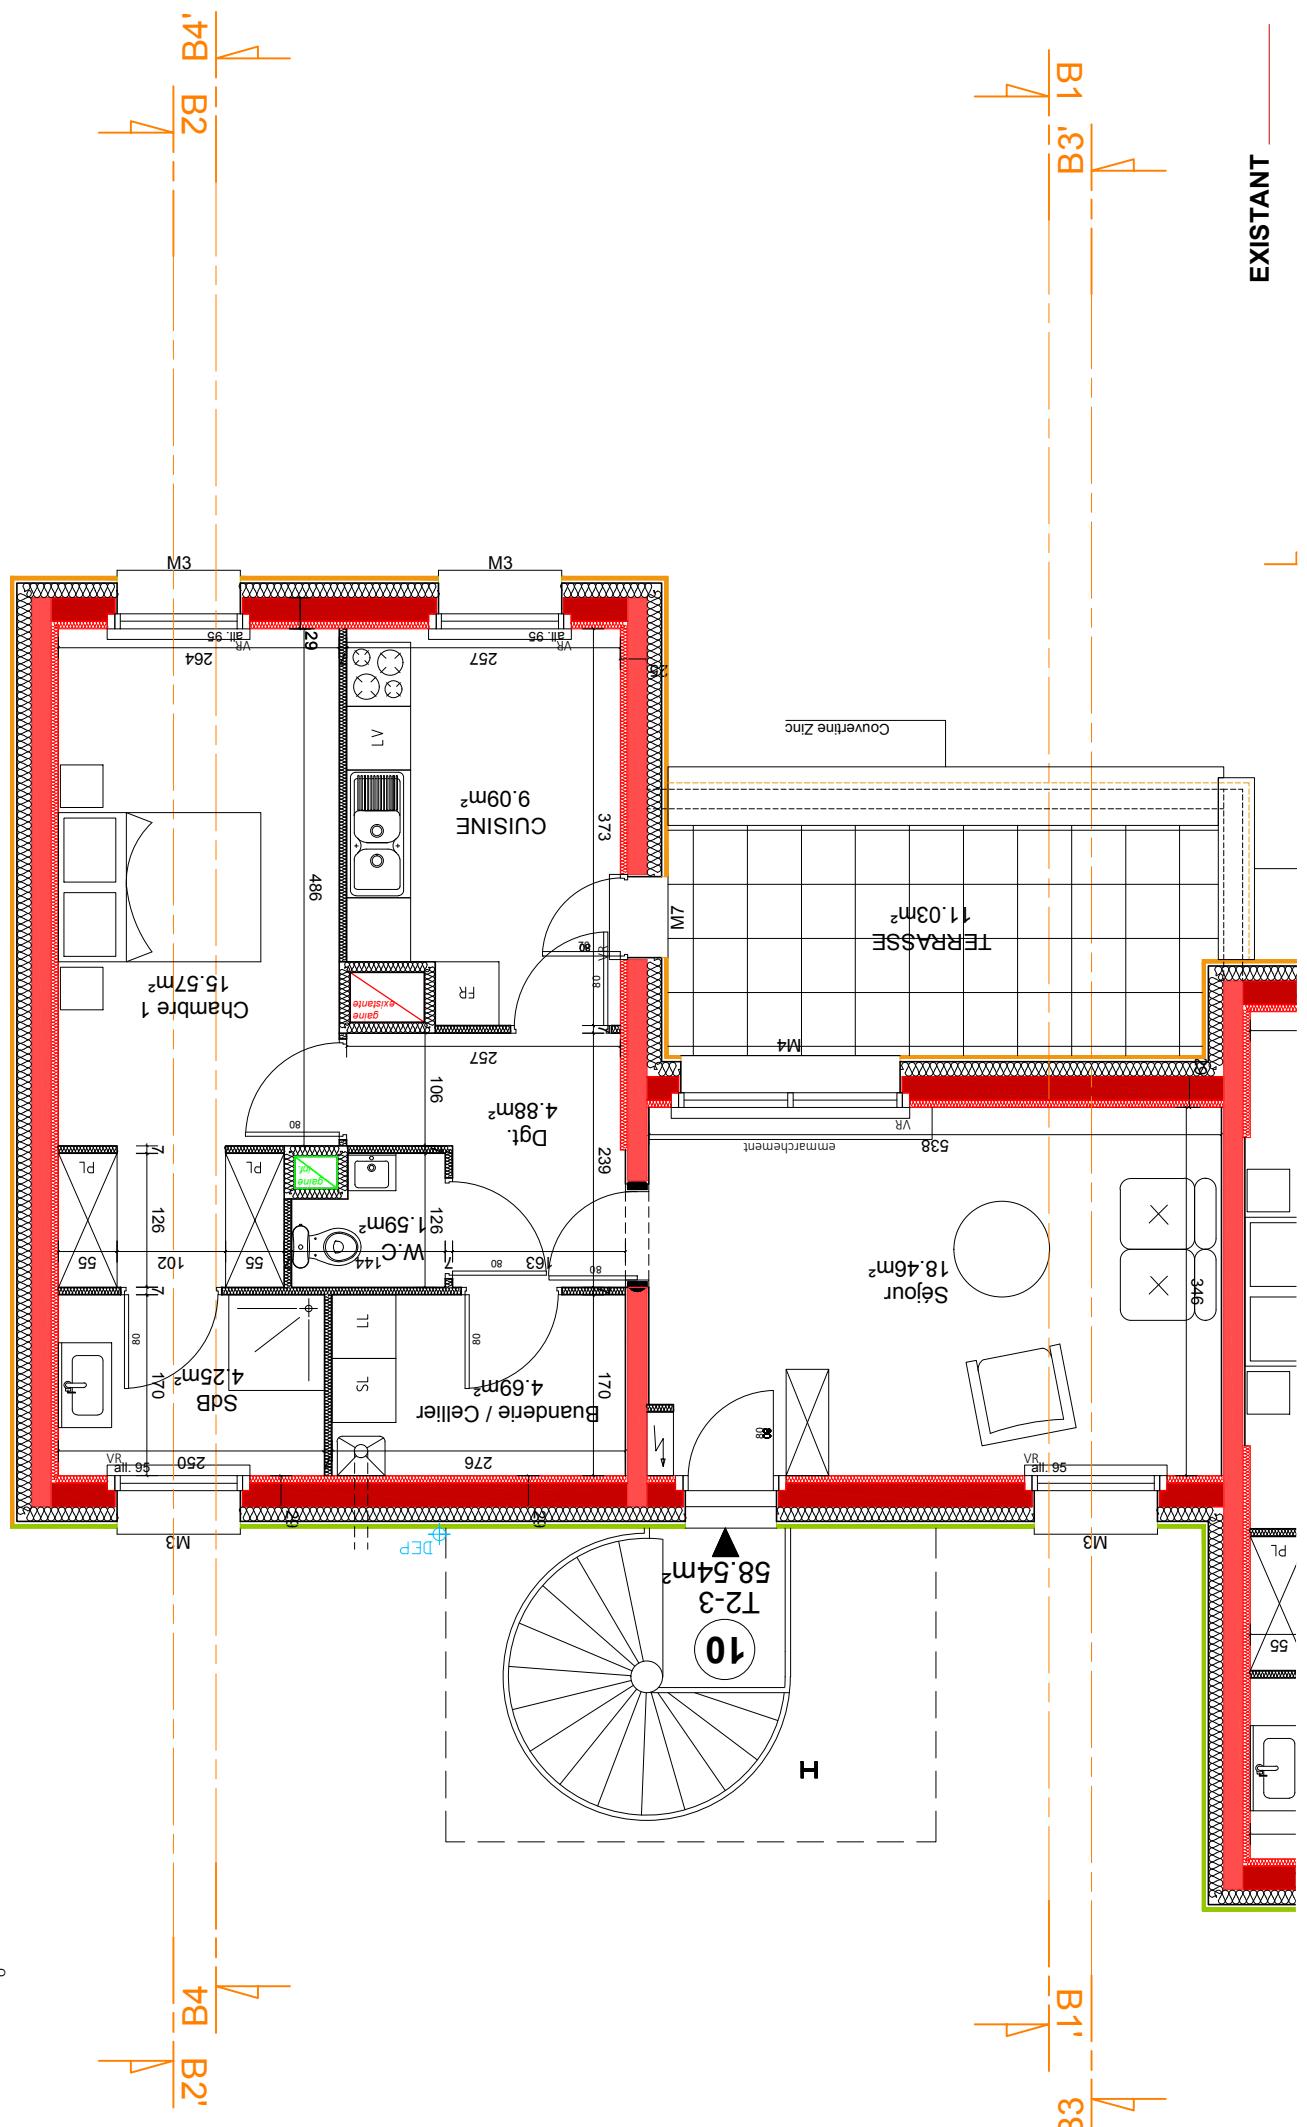

PLAN DE TOITURE - Bâtiment 4
- $n^{\circ} 10$
Ech : 1/50

EXISTANT

16

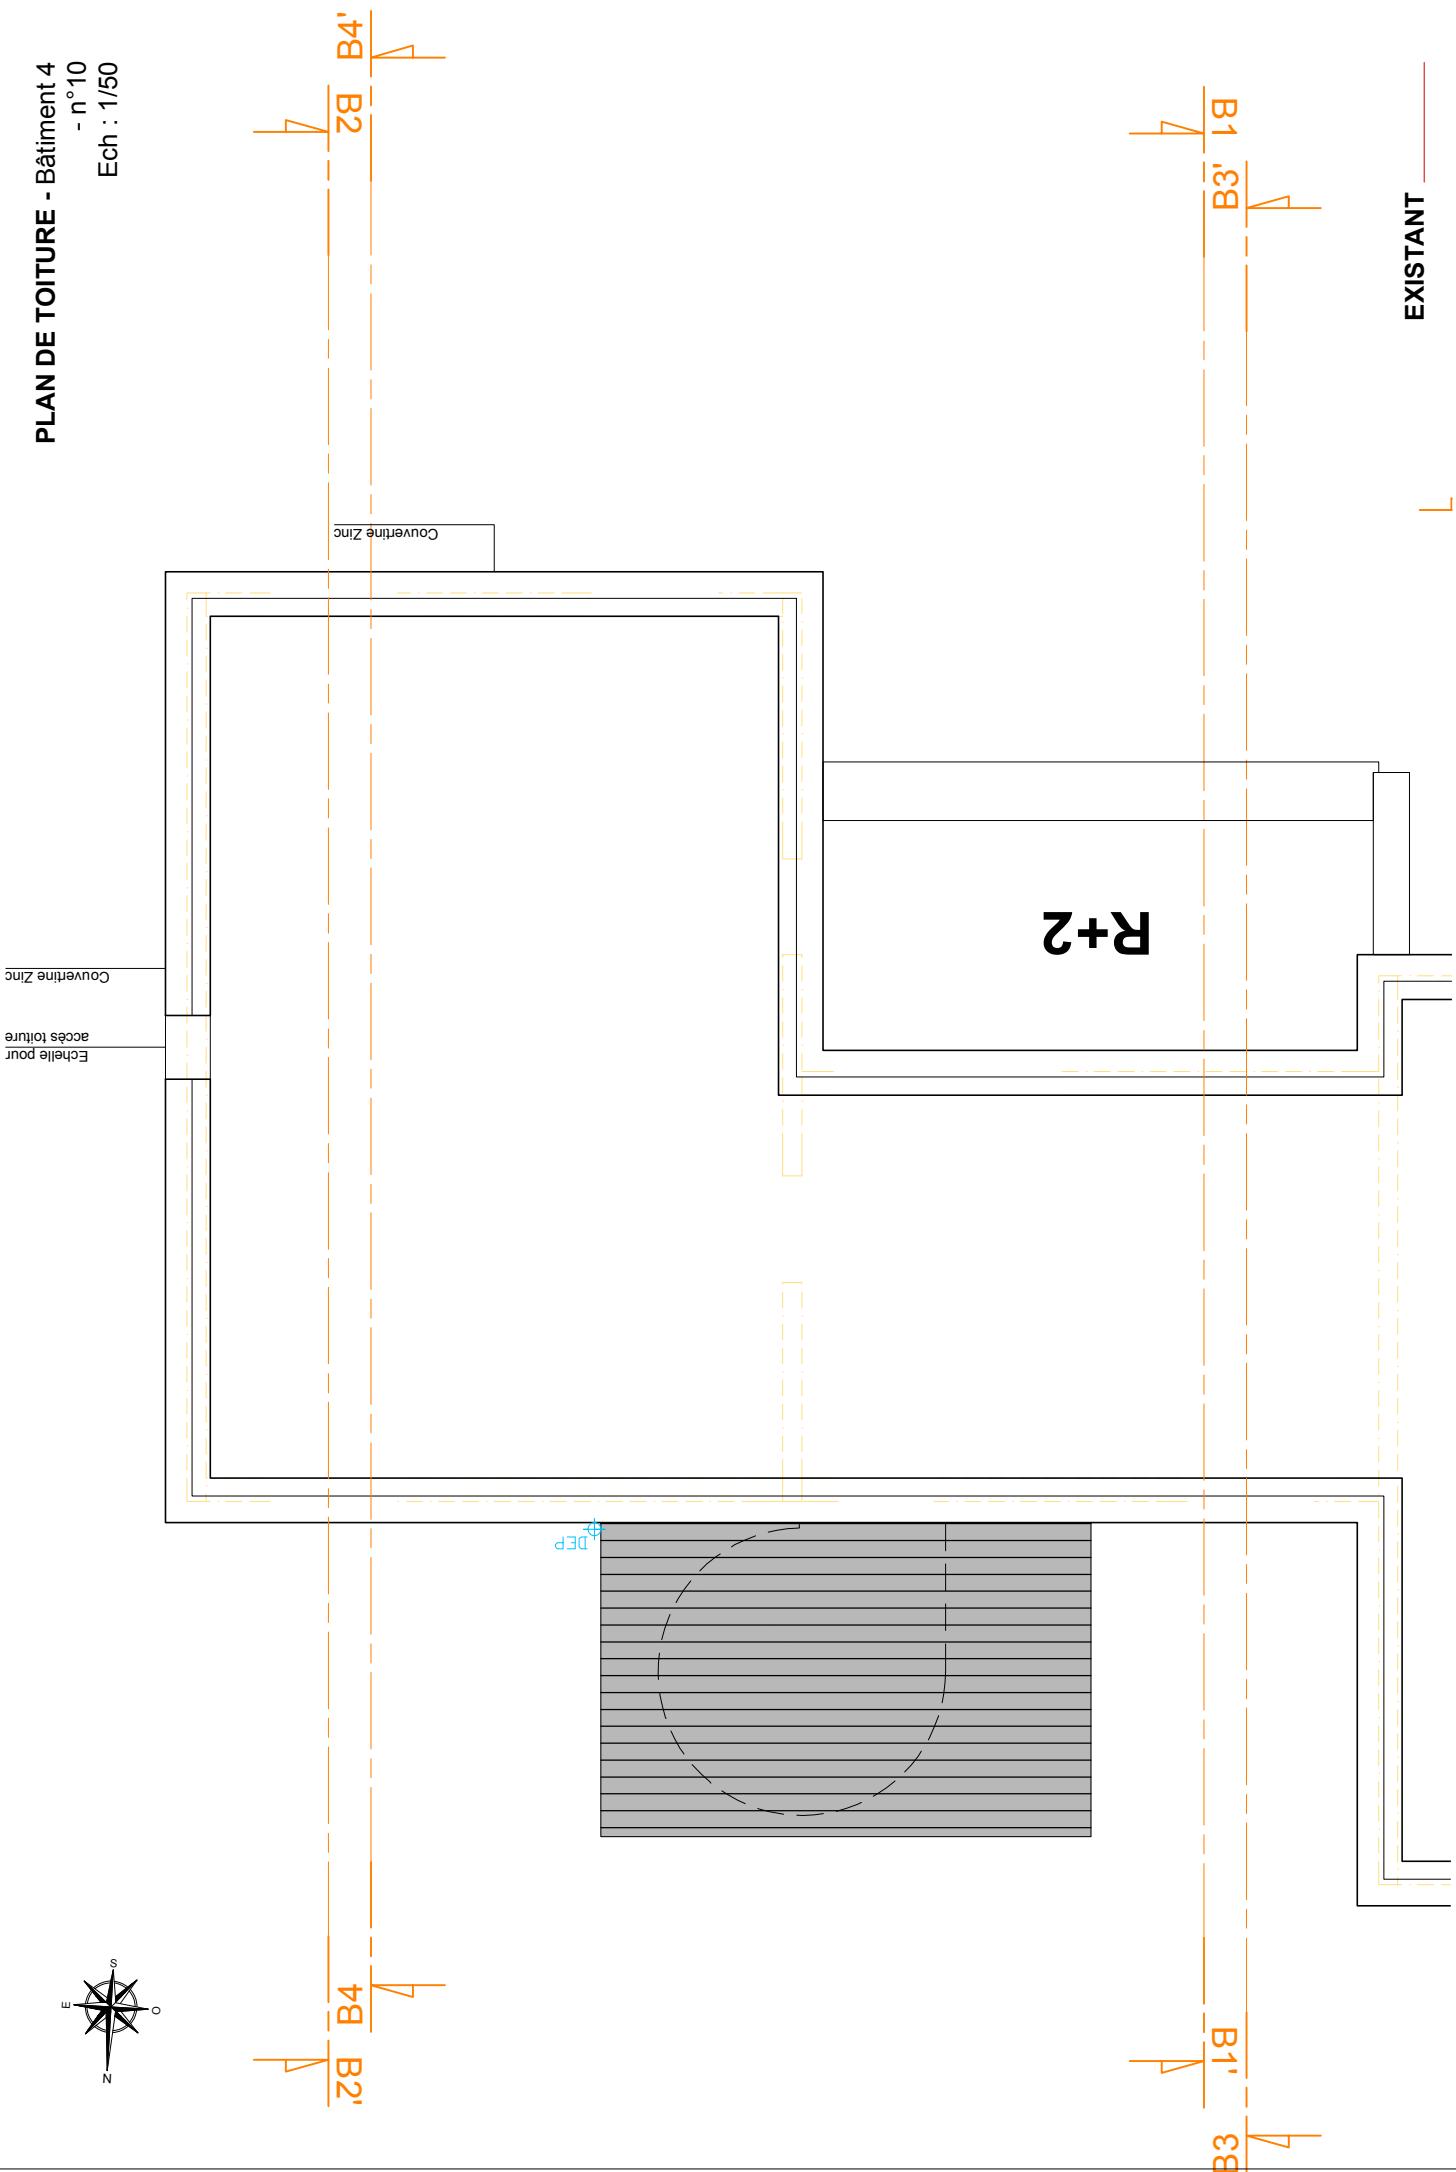

COUPE A1A1' - Bâtiment 4 - n°8
Ech : 1/50

±88,47 **Acrotère**

±87,48 **Egout**

±84,66 **R+2**

±81,96 **R+1**


±79,26 **RDC**


±76,56 **RDU**

±76,92

habillage acier
habillage fibrociment
habillage bois
habillage alu laqué


EXISTANT

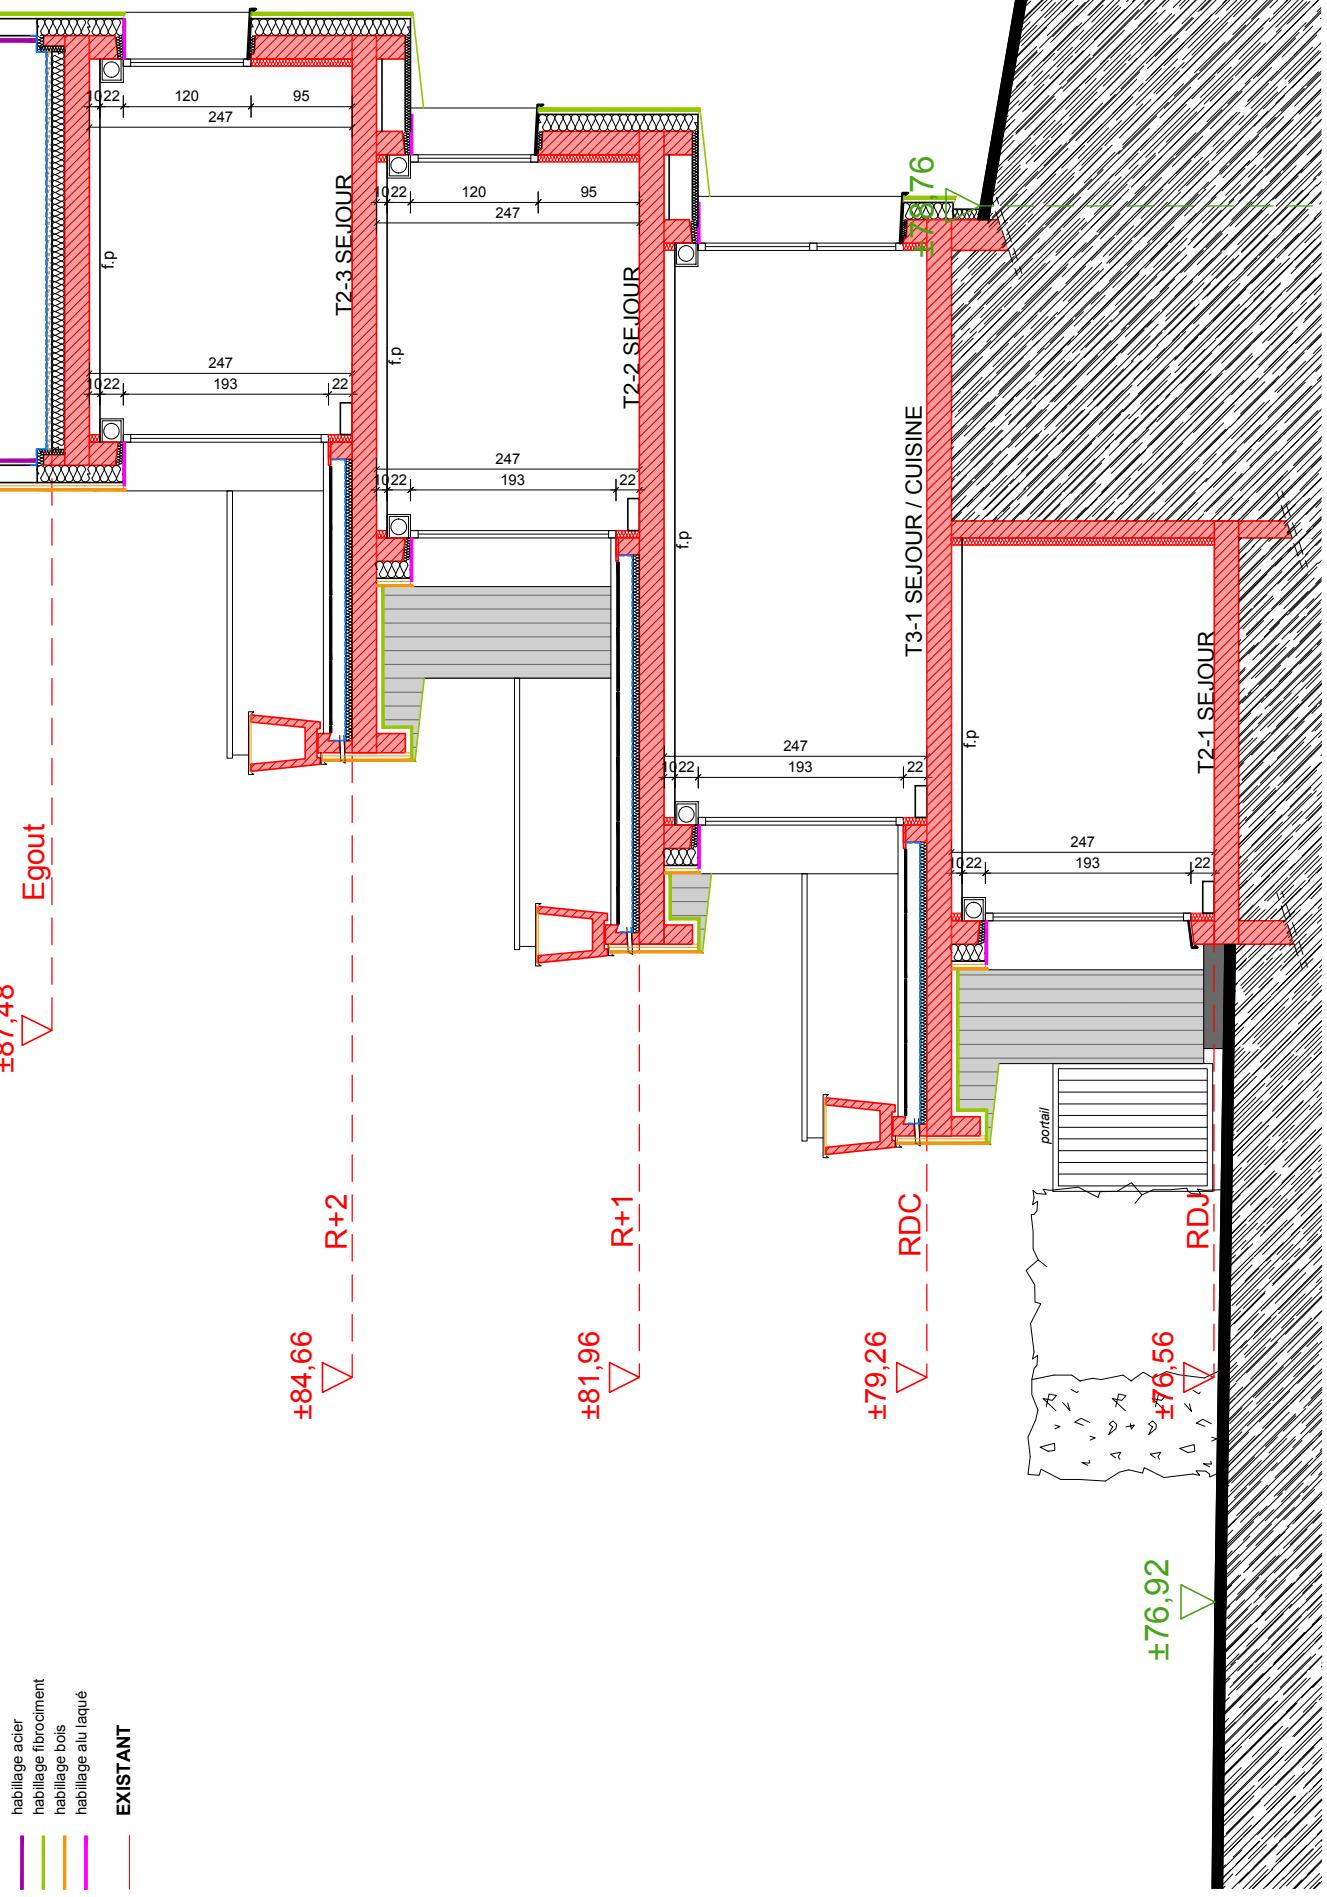

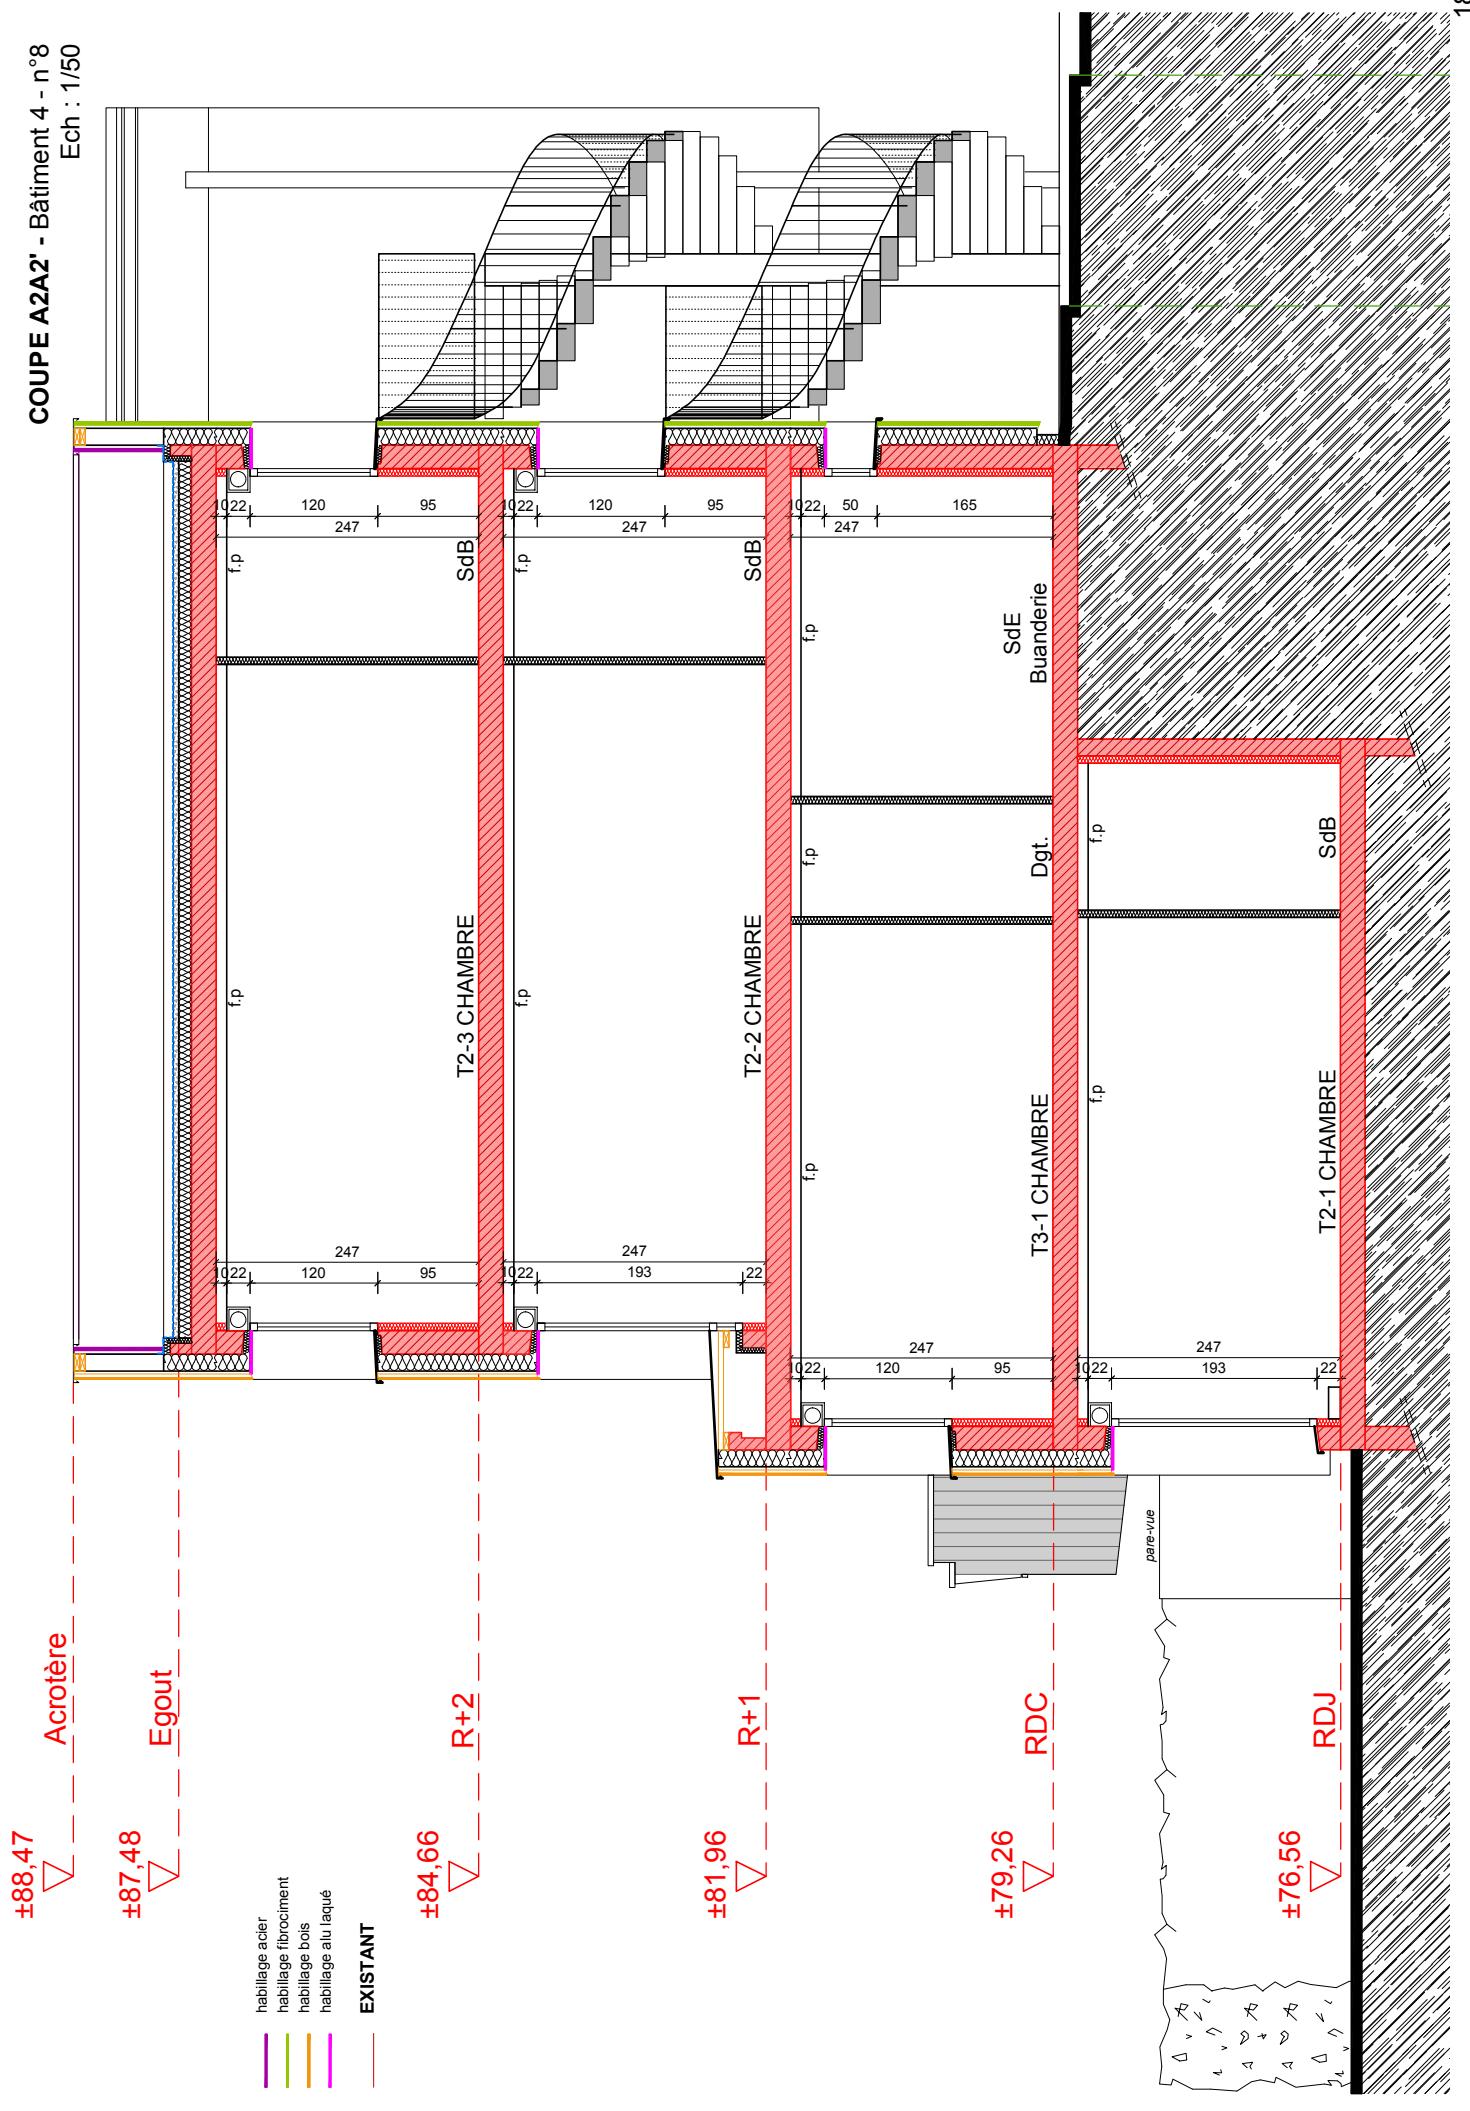


COUPE A3A3' - Bâtiment 4 - n°8
Ech : 1/50


+88,47
Acrotière
+87,48
Egout

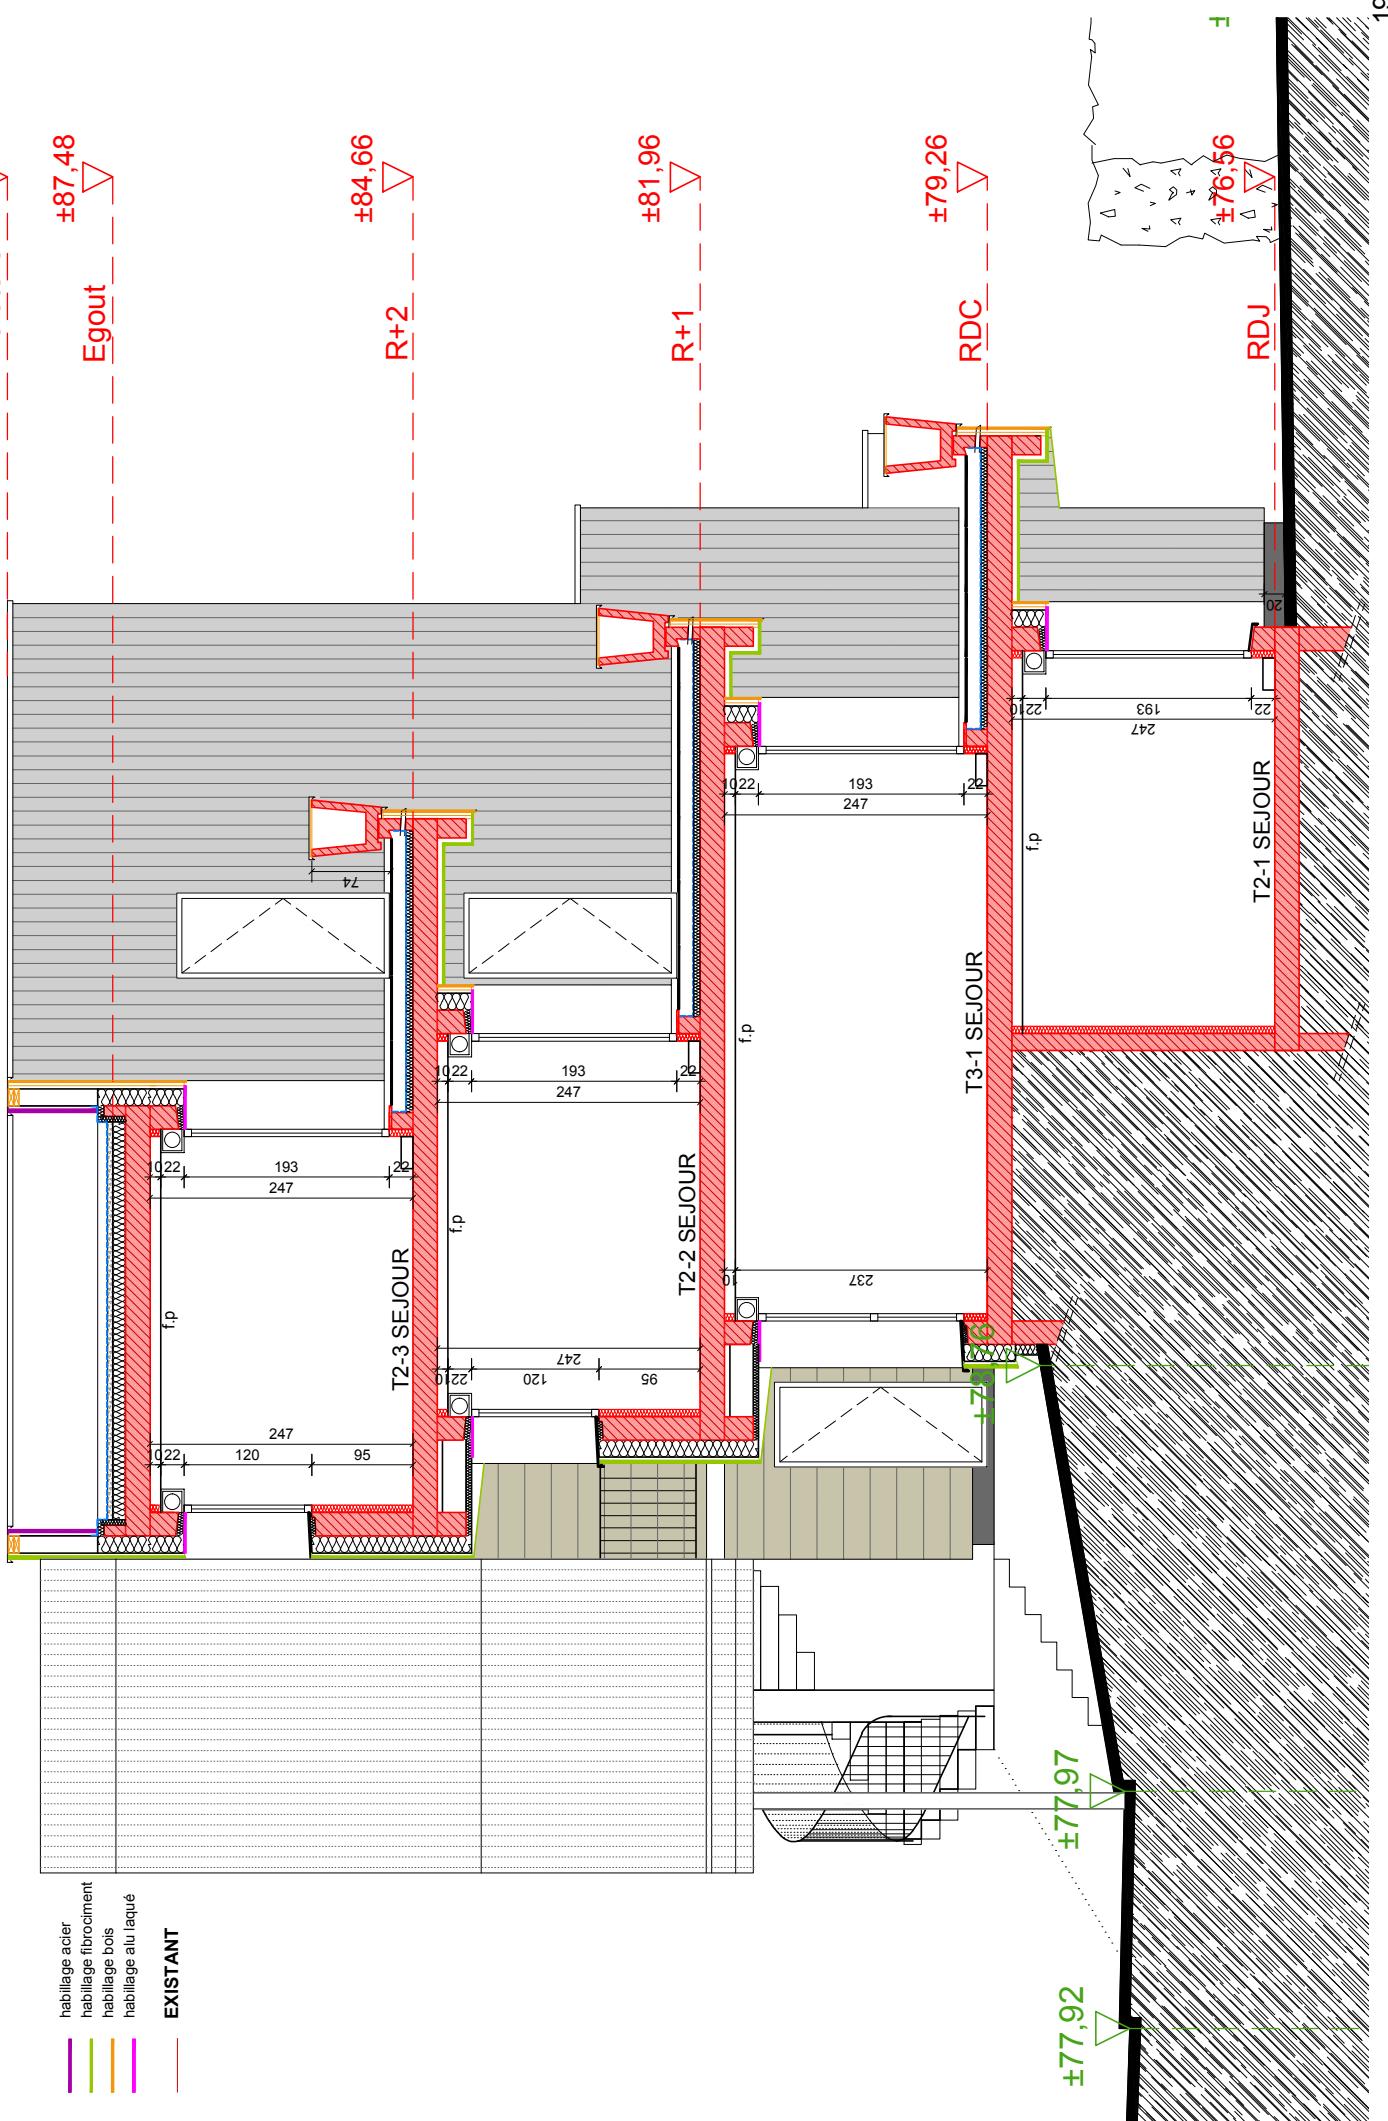

COUPE A4A4' - Bâtiment 4 - n°8
Ech : 1/50

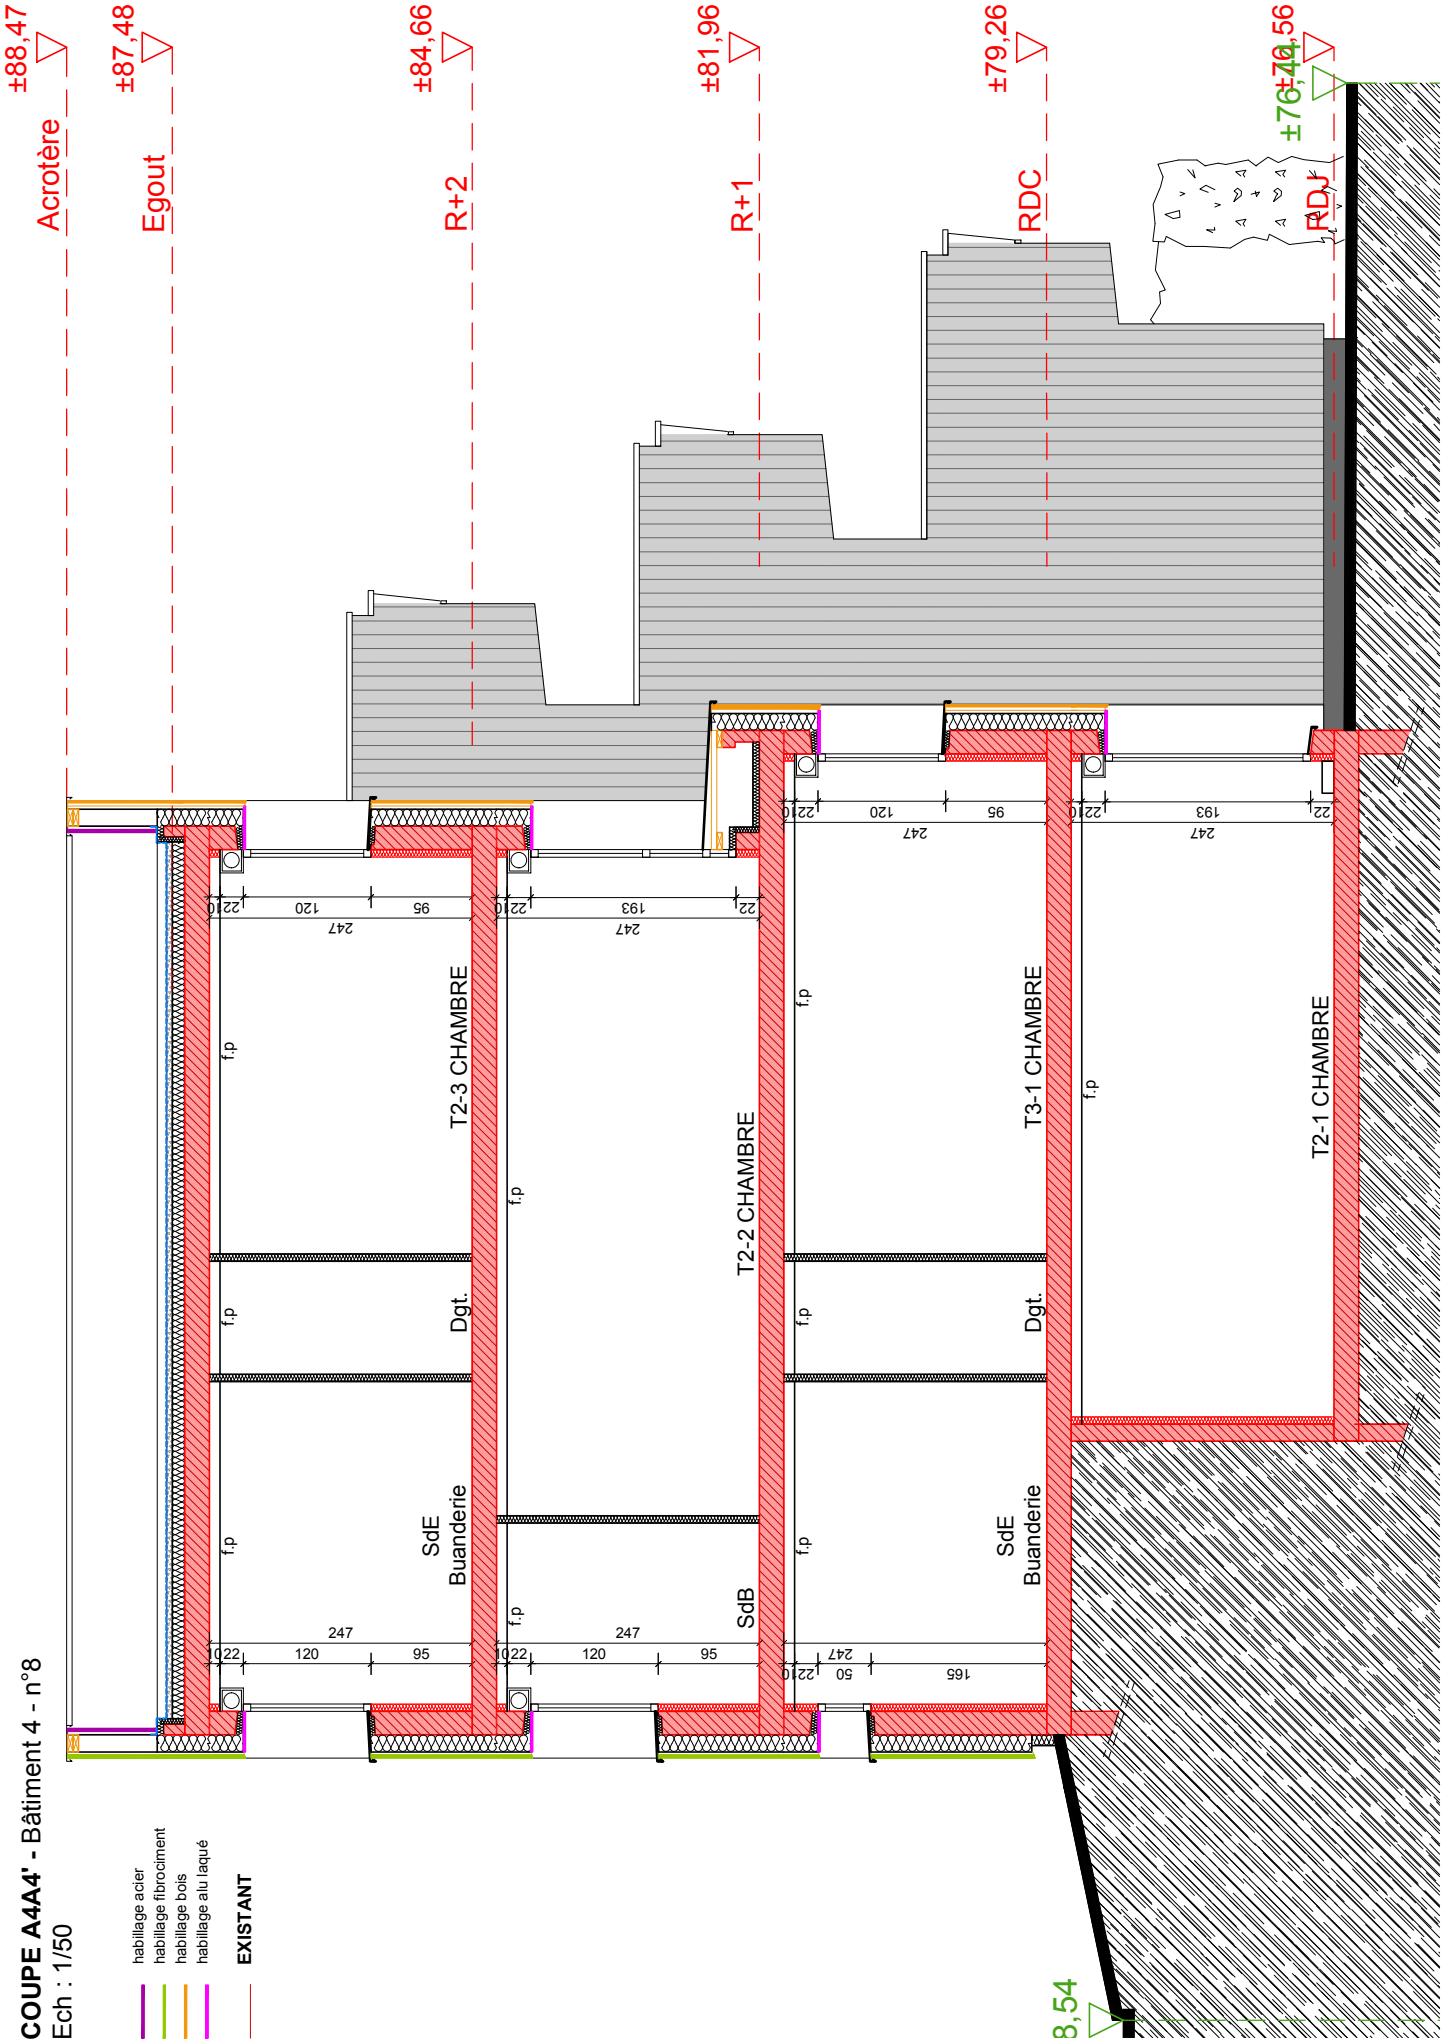


COUPE B1B1' - Bâtiment 4 - n°10
Ech : 1/50

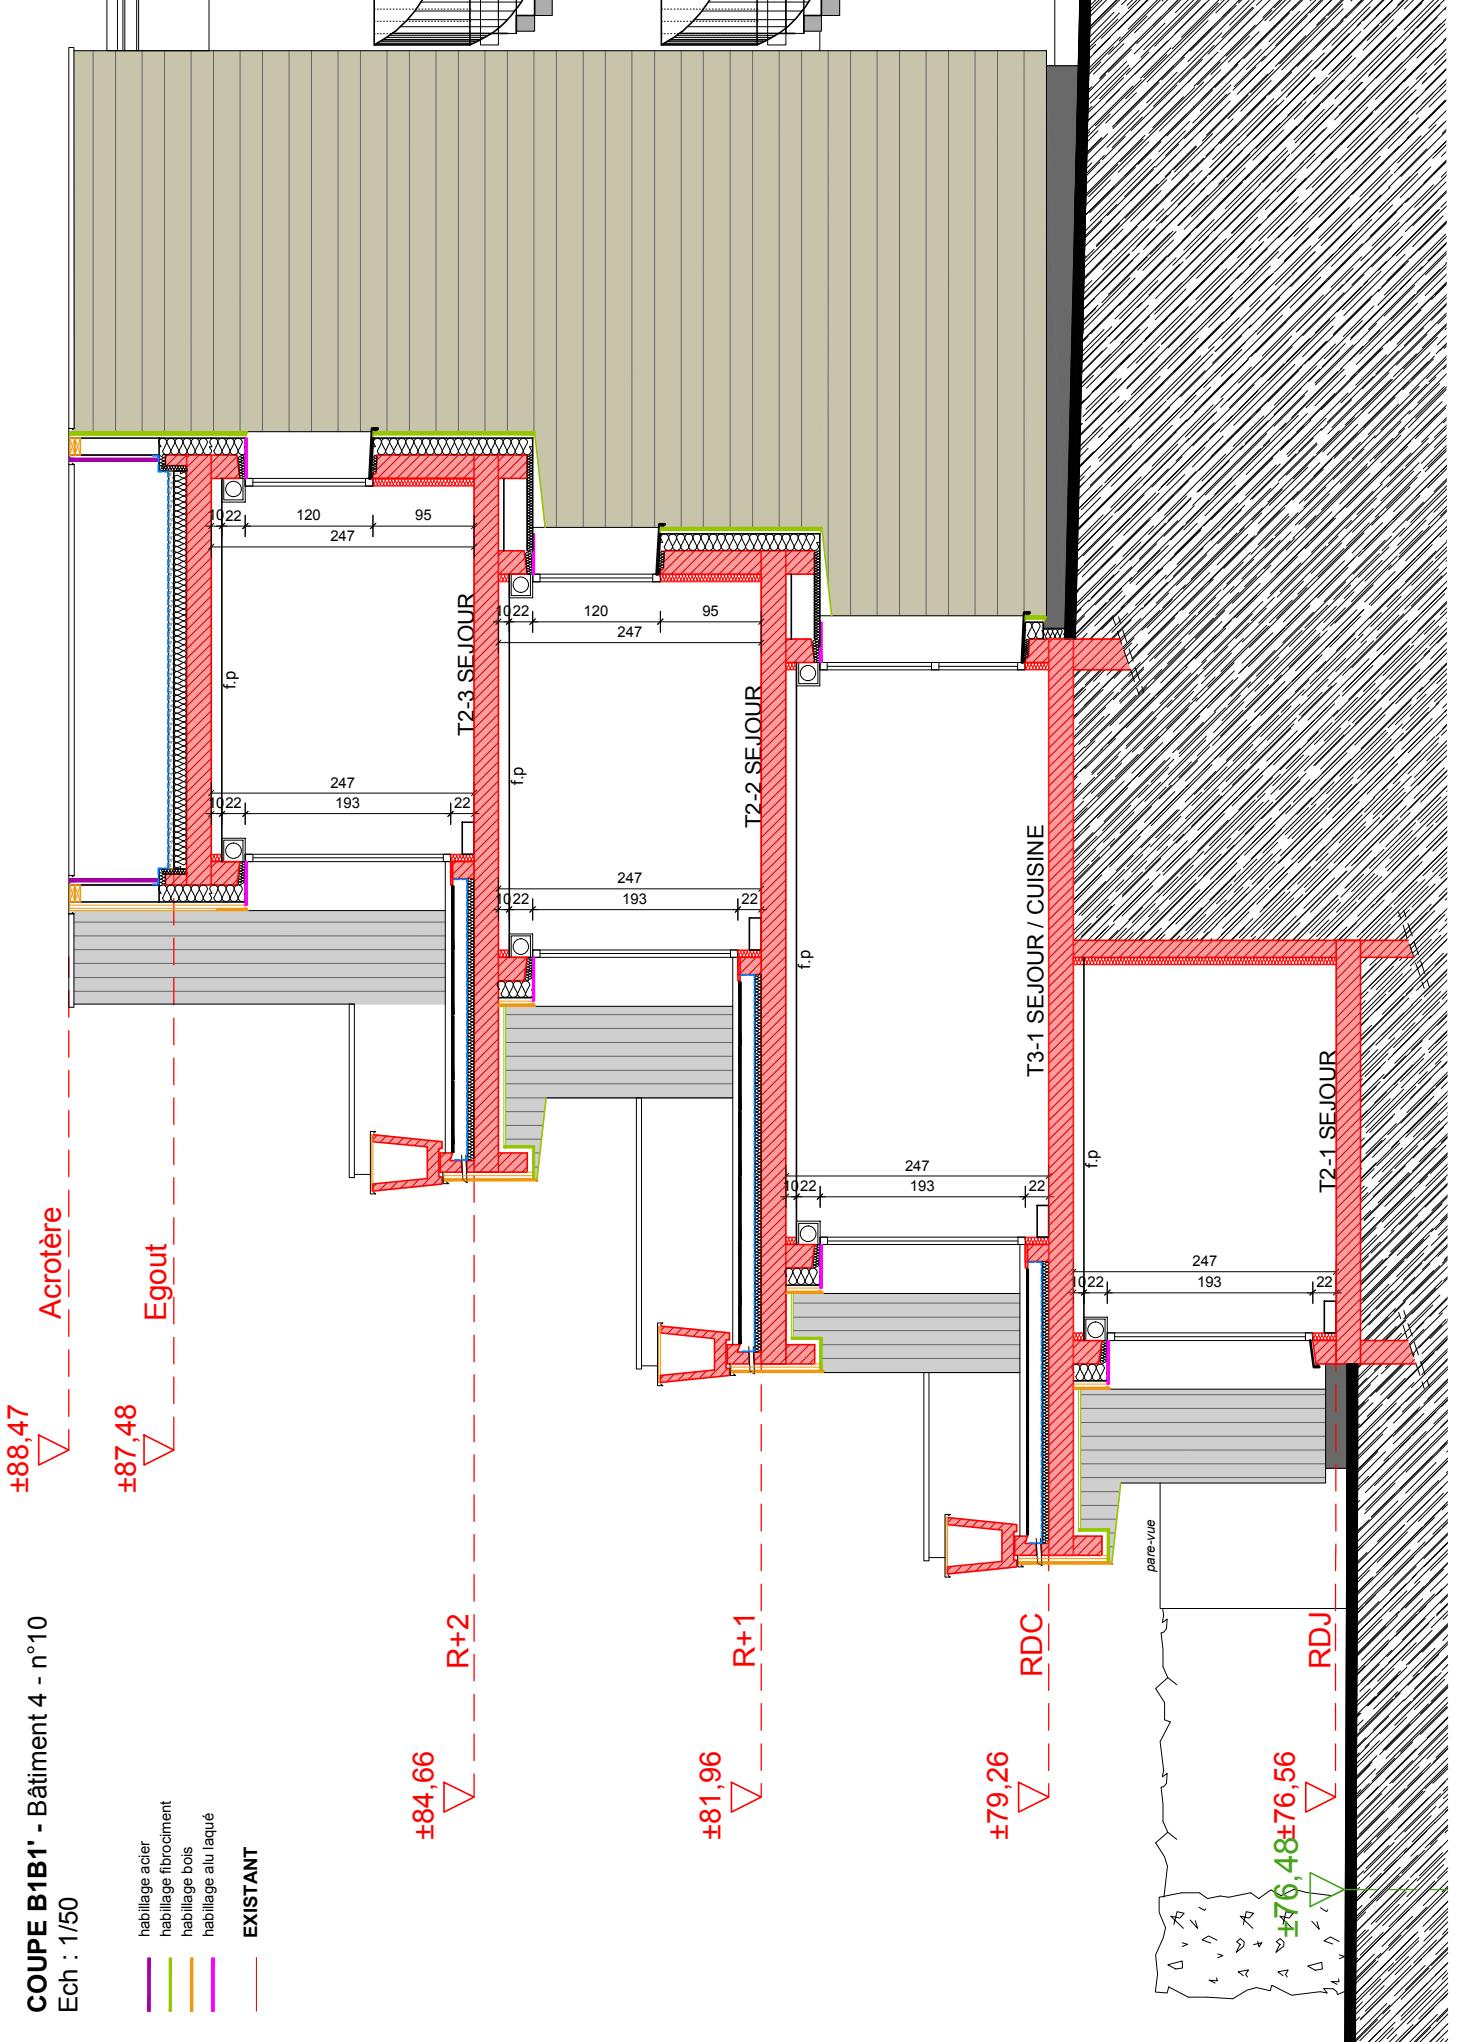


COUPE B2B2' - Bâtiment 4 - n°10
Ech : 1/50

Ech : 1/50

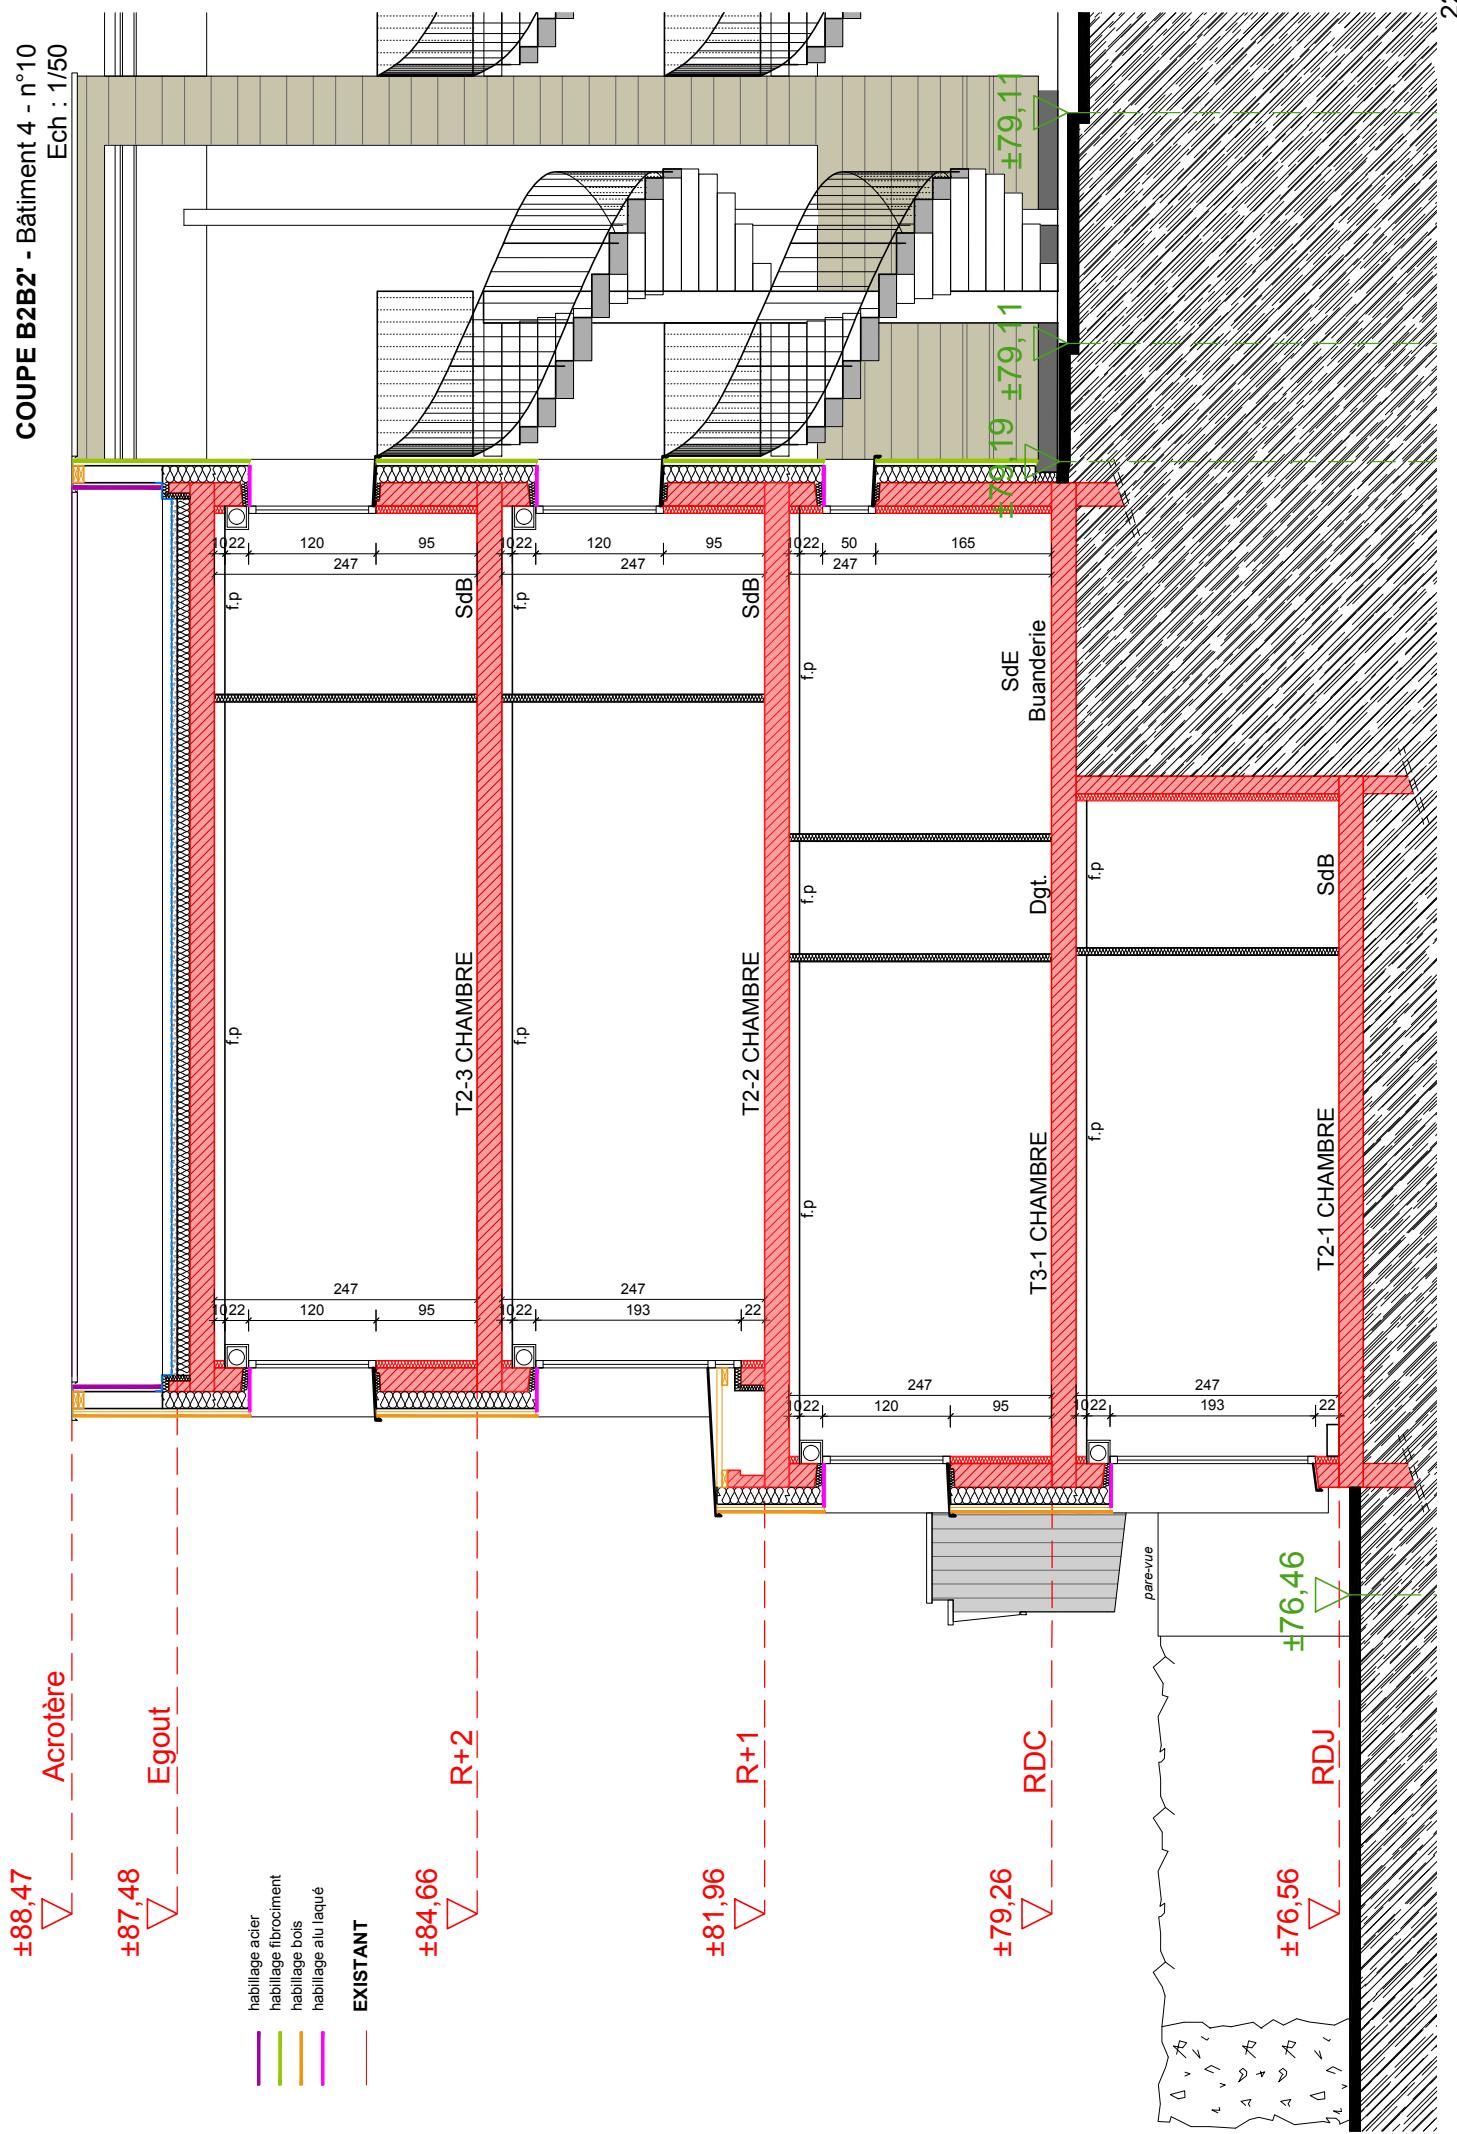


COUPE B3B3' - Bâtiment 4 - n°10
Ech : 1/50

Ech : 1/50

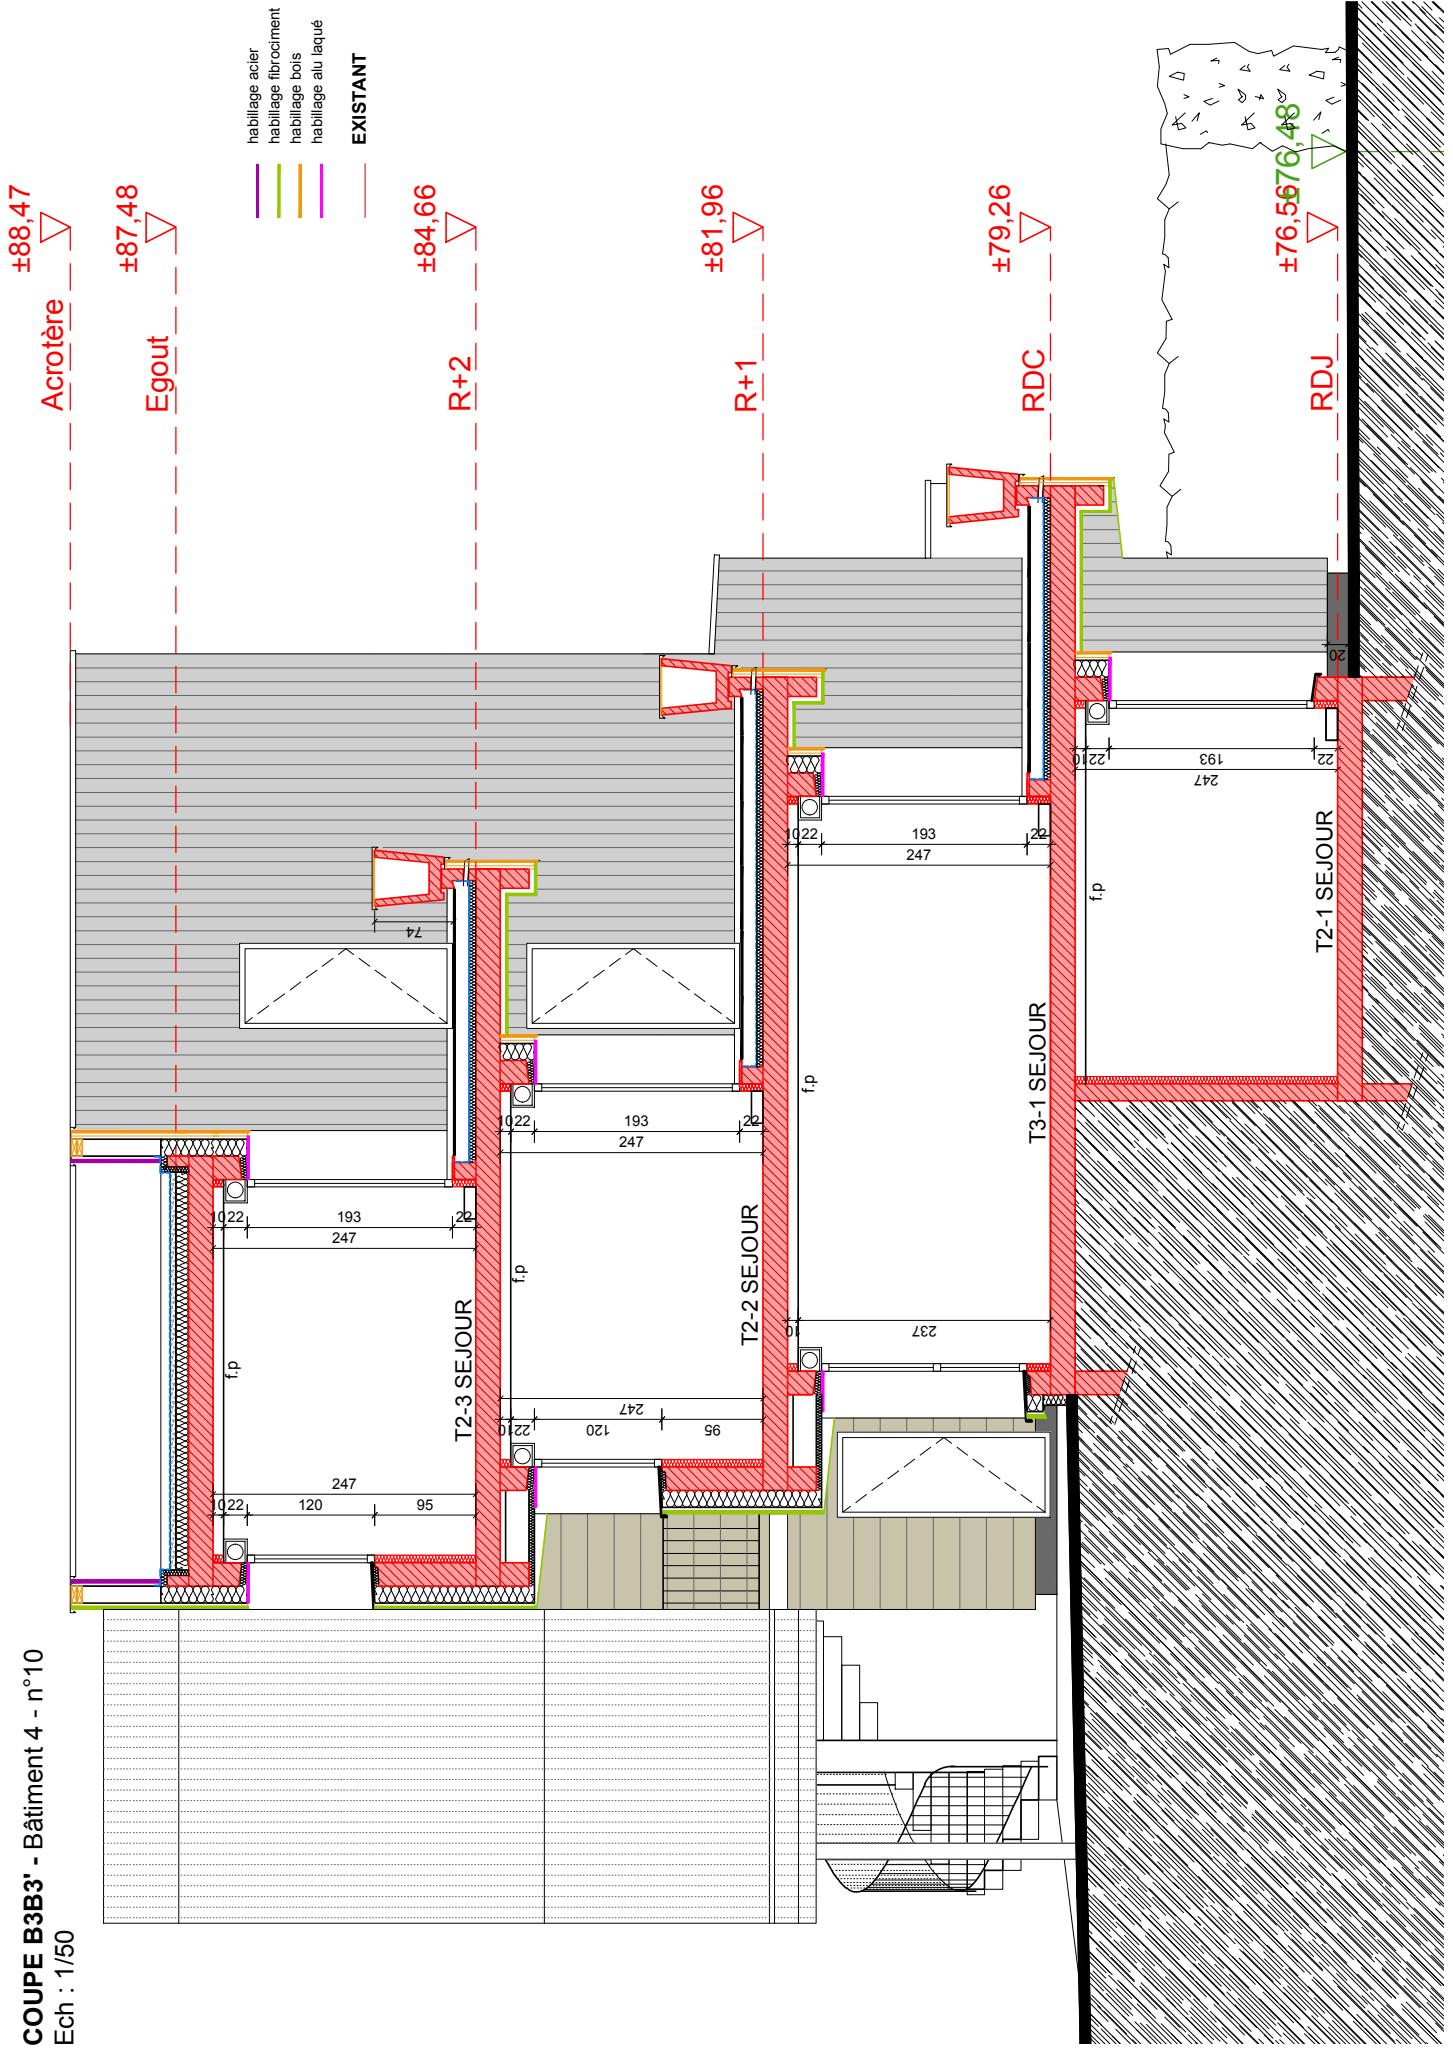


COUPE B4B4' - Bâtiment 4 - n°10
Ech : 1/50

Ech : 1/50

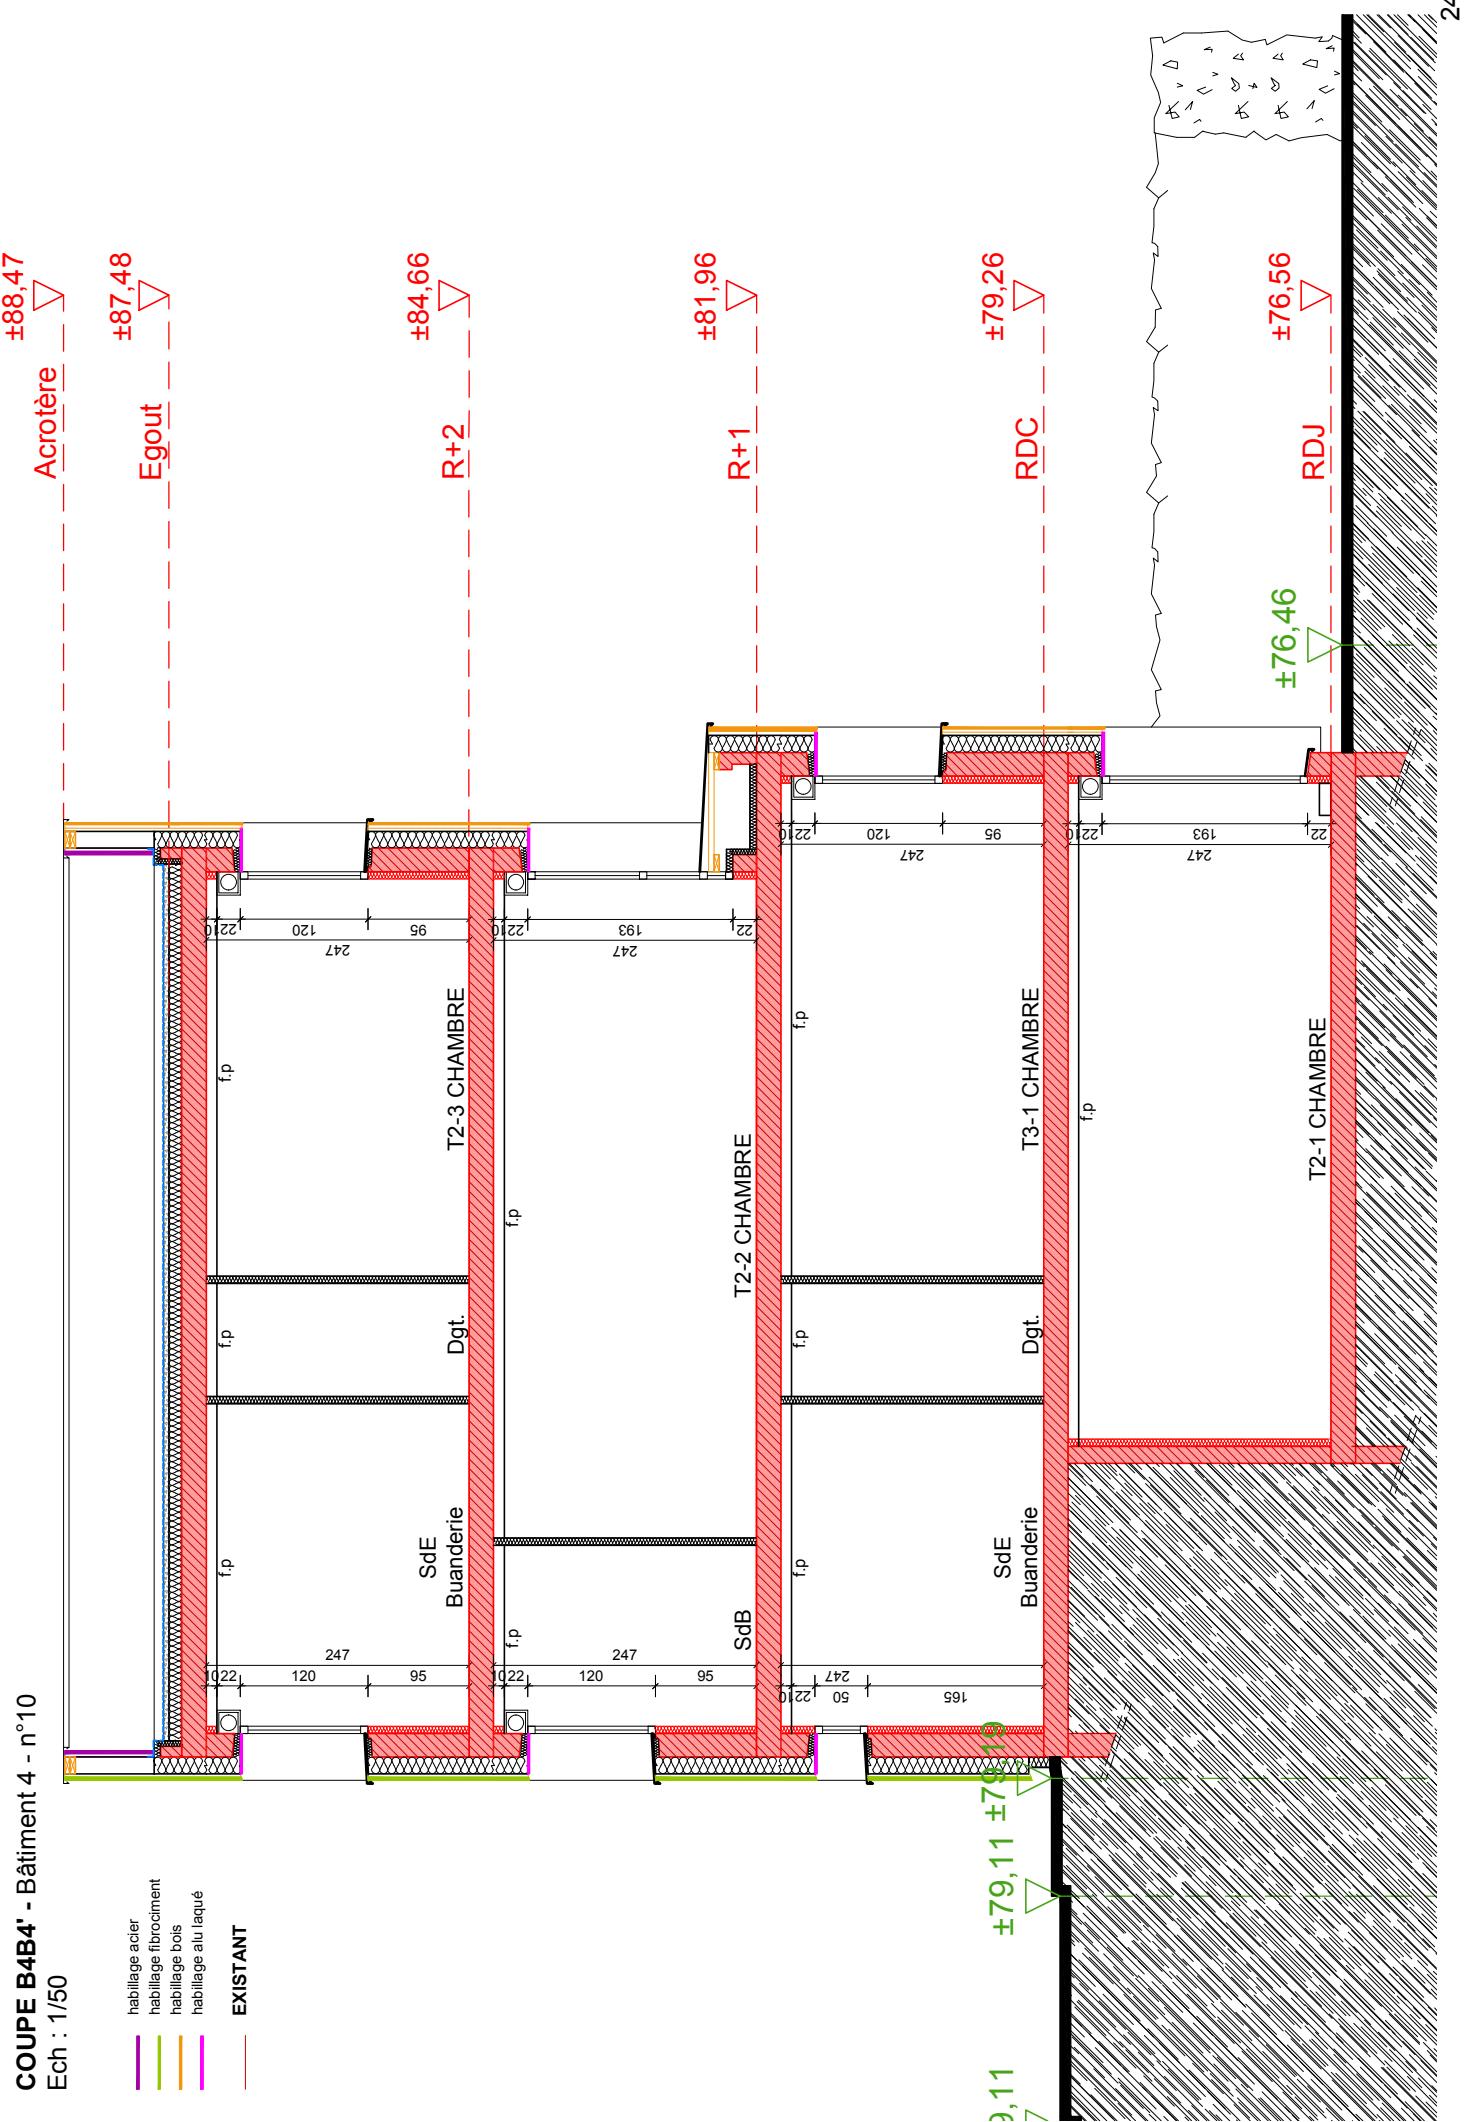

FACADE NORD - Bâtiment 4 - n°8-10
Ech : 1/100

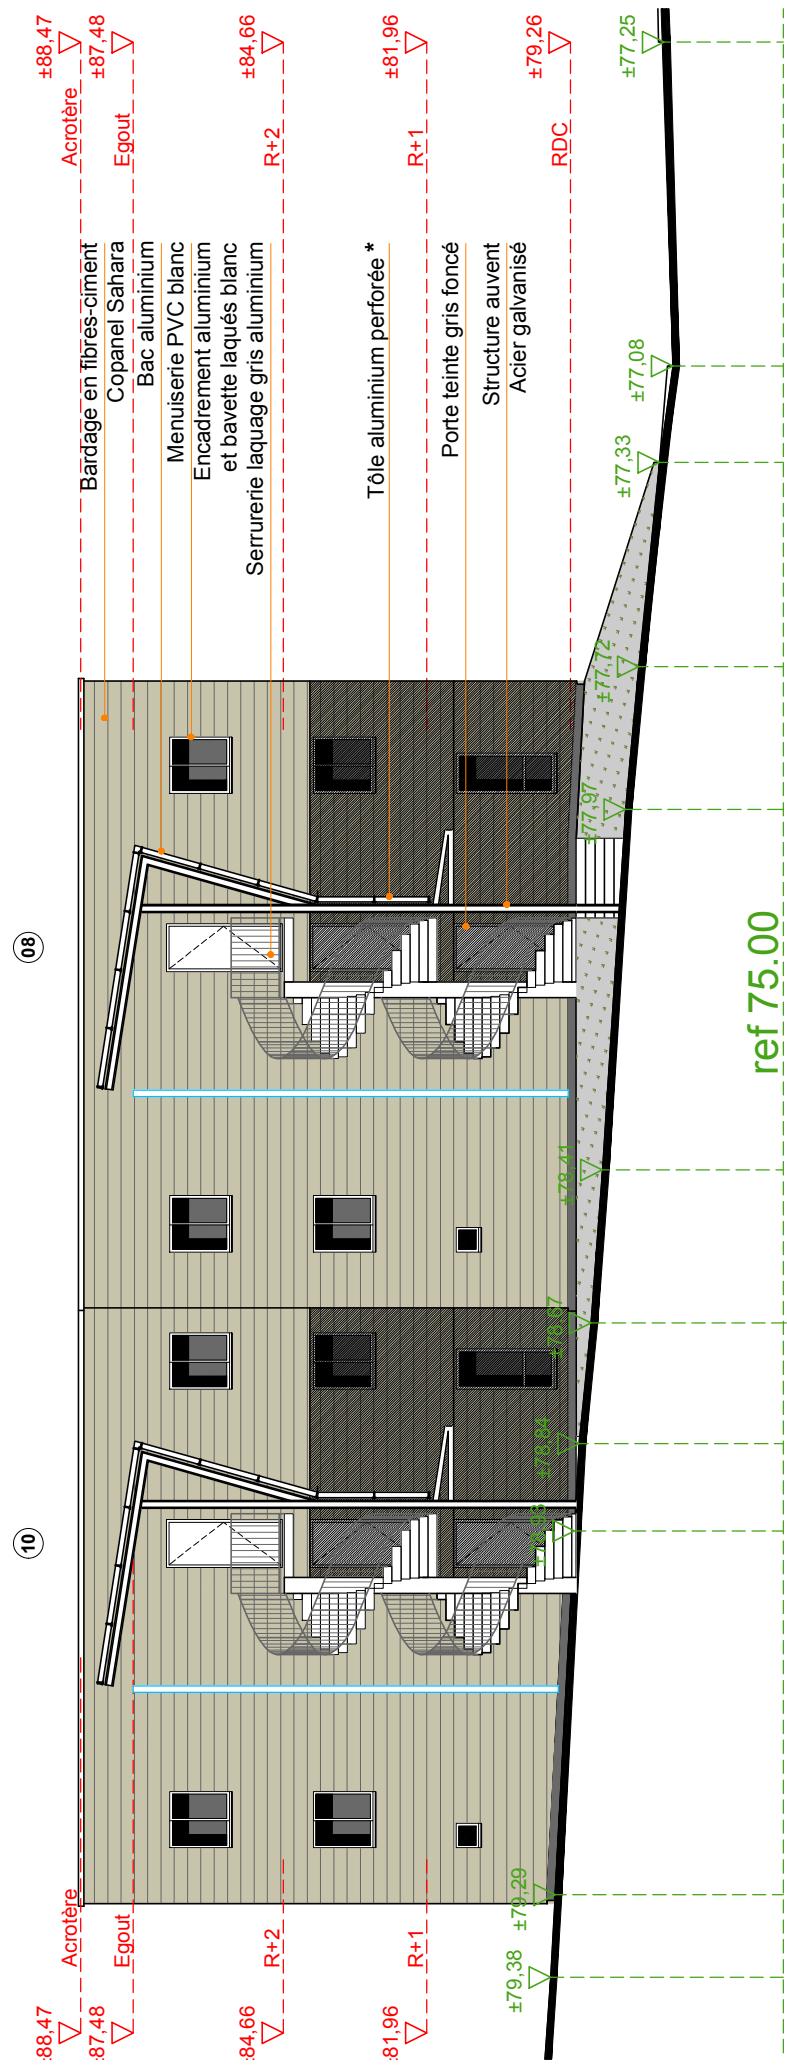


* reproduisant la photographie d'écrivaines célèbres
Elsa Triolet... (liste des 13 écrivaines à faire valider par le maître d'ouvrage et Le Mans Métropole)


FACADE SUD - Bâtiment 4 - n°8-10
Ech : 1/100



FACADE EST - Bâtiment 4 - n°8-10
Ech : 1/100

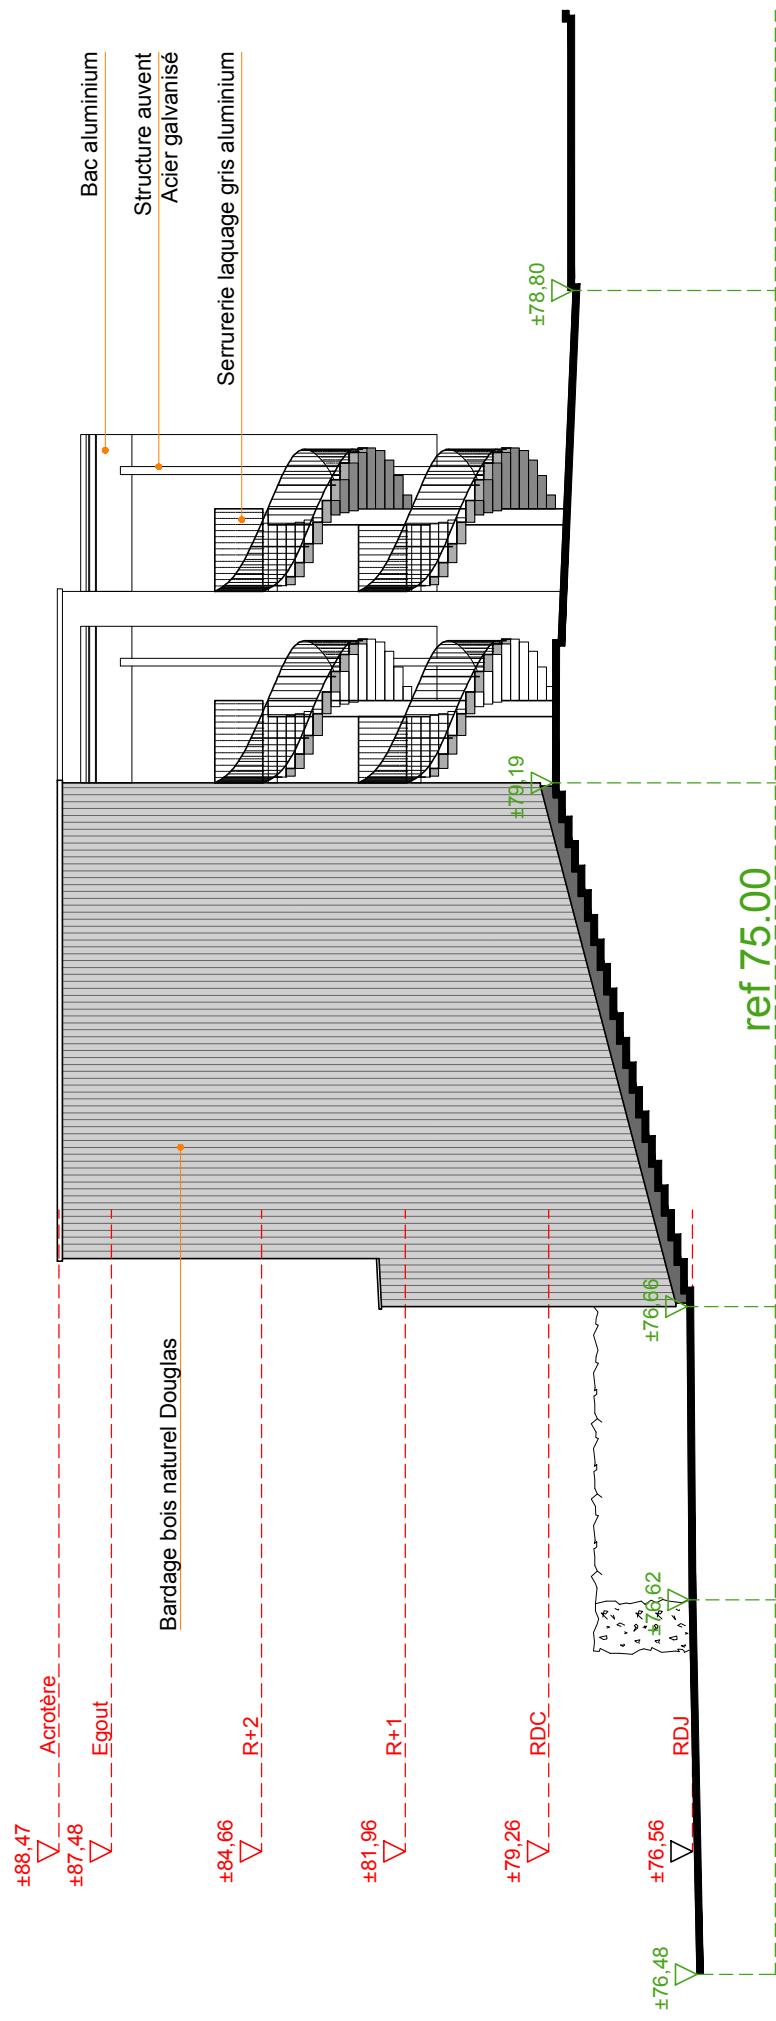

FACADE OUEST - Bâtiment 4 - n°8-10
Ech : 1/100

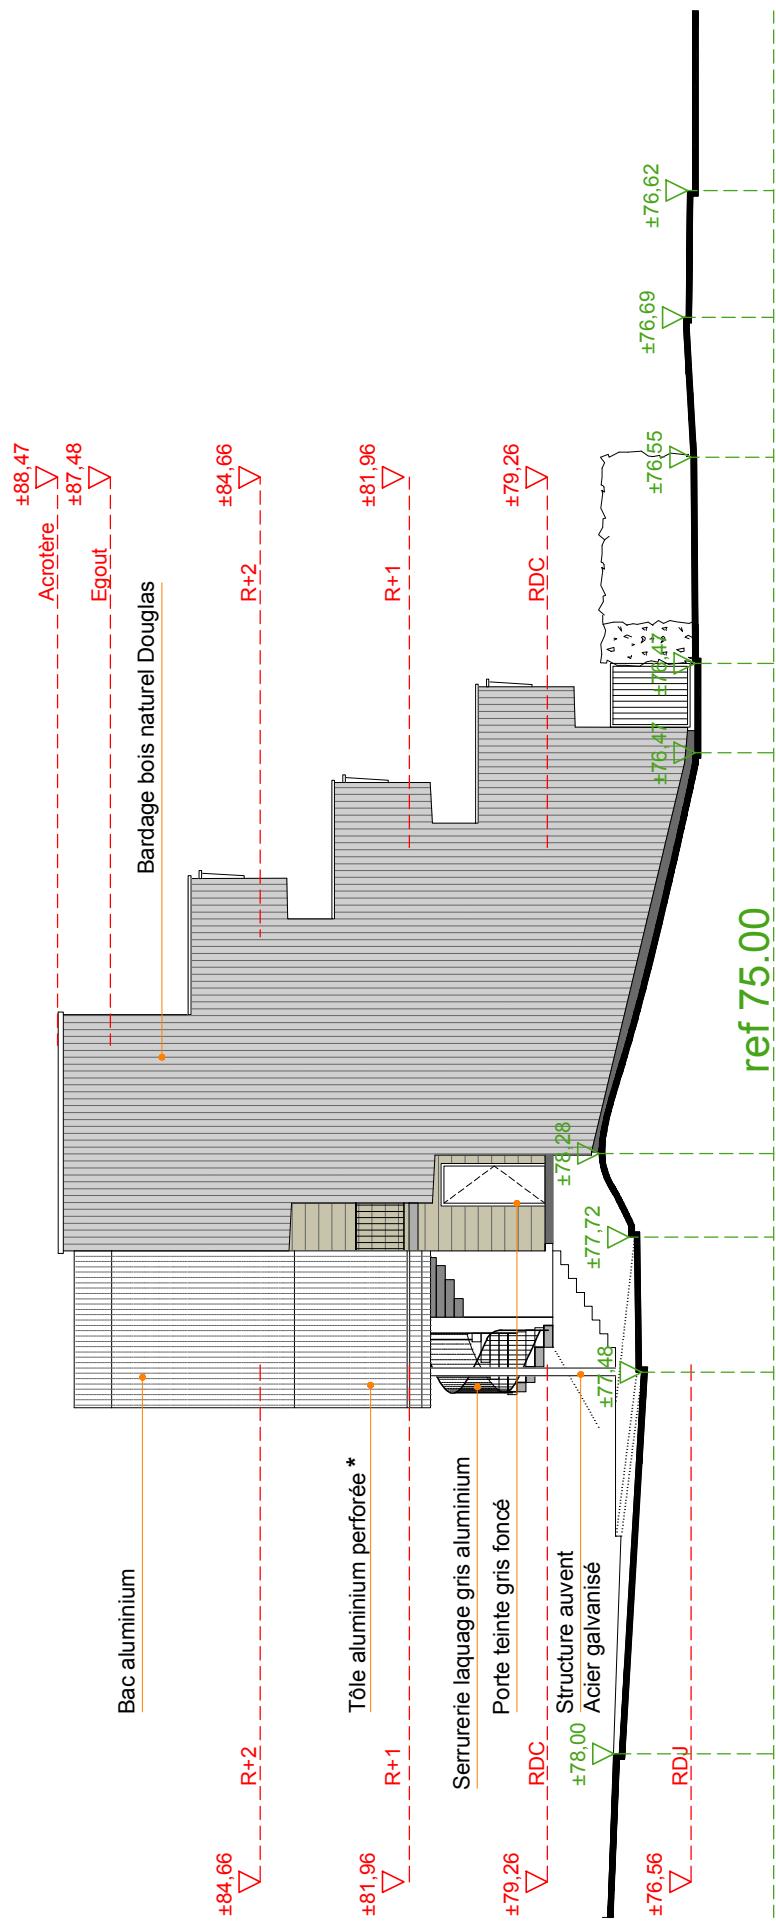

* reproduisant la photographie d'écrivaines célèbres
Elsa Triolet... (liste des 13 écrivaines à faire valider par le maître d'ouvrage et Le Mans Métropole)